



PORTFOLIO

DORIS WANJIRU NG'ANGA
THE TECHNICAL UNIVERSITY OF KENYA

RESUME



DORIS WANJIRU NG'ANG'A

PHONE :0743525095

EMAIL:dorisnganga254@gmail.com

LINKEDIN:<https://www.linkedin.com/in/doris-ng-ang-a-015b10214>

ARCHITECTURE IS IN THE HEART.

I believe that any good design with its users at heart, should be innovative, covering all contemporary issues as well as anticipate the future needs of its users. I am passionate about design and space making, patient, self-driven and willing to go above and beyond to produce quality ideas that can be effectively executed out in the real world.

EDUCATION BACKGROUND

• 2005-2013



JOYLAND ACADEMY
375 MARKS

• 2013-2017



CHINGA GIRLS HIGH SCHOOL
A-

• 2017- PRESENT



TECHNICAL UNIVERSITY OF KENYA

LANGUAGES

- English
- Swahili

INTERESTS

- travelling
- drawing
- reading
- music
- furniture design

SKILLS

- design
- model making
- typical analysis
- critical observation

OBJECTIVE

To join an architectural firm which avails an opportunity to learn, enhance my professional capabilities, and contribute in a creative work environment .In spite of that, to simultaneously expand my skillsets and getting broader exposure to the field .It would be my endeavour to establish myself as a valuable asset to the organization which would best utilize my expertise as an intern.

TECHNICAL SKILLS

AUDOTESK REVIT



LUMION



ARCHICAD



ENSCAPE



SKETCH -UP



TWINMOTION



ADOBE PHOTOSHOP



ADOBE INDESIGN



AUTOCAD



MS POWERPOINT



MS EXCEL



MS WORD



PERSONAL SKILLS

- Effective Written & Oral Communication
- Teamwork
- Creativity & Problem Solving
- Critical Thinking

PARTICIPATIONS

1. Attachment at Dreams plan & services
- 2.Attachment at Kiambu county government , DEPARTMENT OF LAND, HOUSING, PHYSICAL PLANNING
3. online classes on sustainable buildings from 11th-15th january 2021
4. AAK webinar on covid 19 prep 24th april 2020

REFERENCES AVAILABLE UPON REQUEST

CONTENT

01. MIXED USE DEVELOPMENT
2024// INDUSTRIAL AREA, NAIROBI

02. AFFORDABLE HOUSING
2023//KALOLENI, NAIROBI

03. URBAN HOUSING CLUSTER DESIGN
2022// BANANA,KIAMBU COUNTY

04. ECO-LODGE DESIGN
2022//NAIROBI, KENYA

05. LANDSCAPE DESIGN
2020-2023




MASTERPLAN BRIEF

The city of Nairobi is currently undergoing some redevelopment. This redevelopment is driven by the changing demands of commerce, recreation, infrastructure, accommodation and entertainment. Railways being near CBD creates opportunities to connect CBD and the neighbouring communities. In the planning and designing of a smart city concepts such as revitalization, redevelopment, renewal, regeneration, integrated urban design, non motorised network and pedestrian movements can be explored. These themes and the five elements of a city will be incorporated to create a smart city.

MASTER PLAN CONCEPT

The project starts with design of a smart city from which a mixed use development is to be designed. The concept for the masterplan is 15 minute district and the site is divided into 5 districts and each district has all the amenities within 15 minute walking distance. All districts are connected with a hexagonal green corridor and lie along the 5 major landmarks of the 5 districts

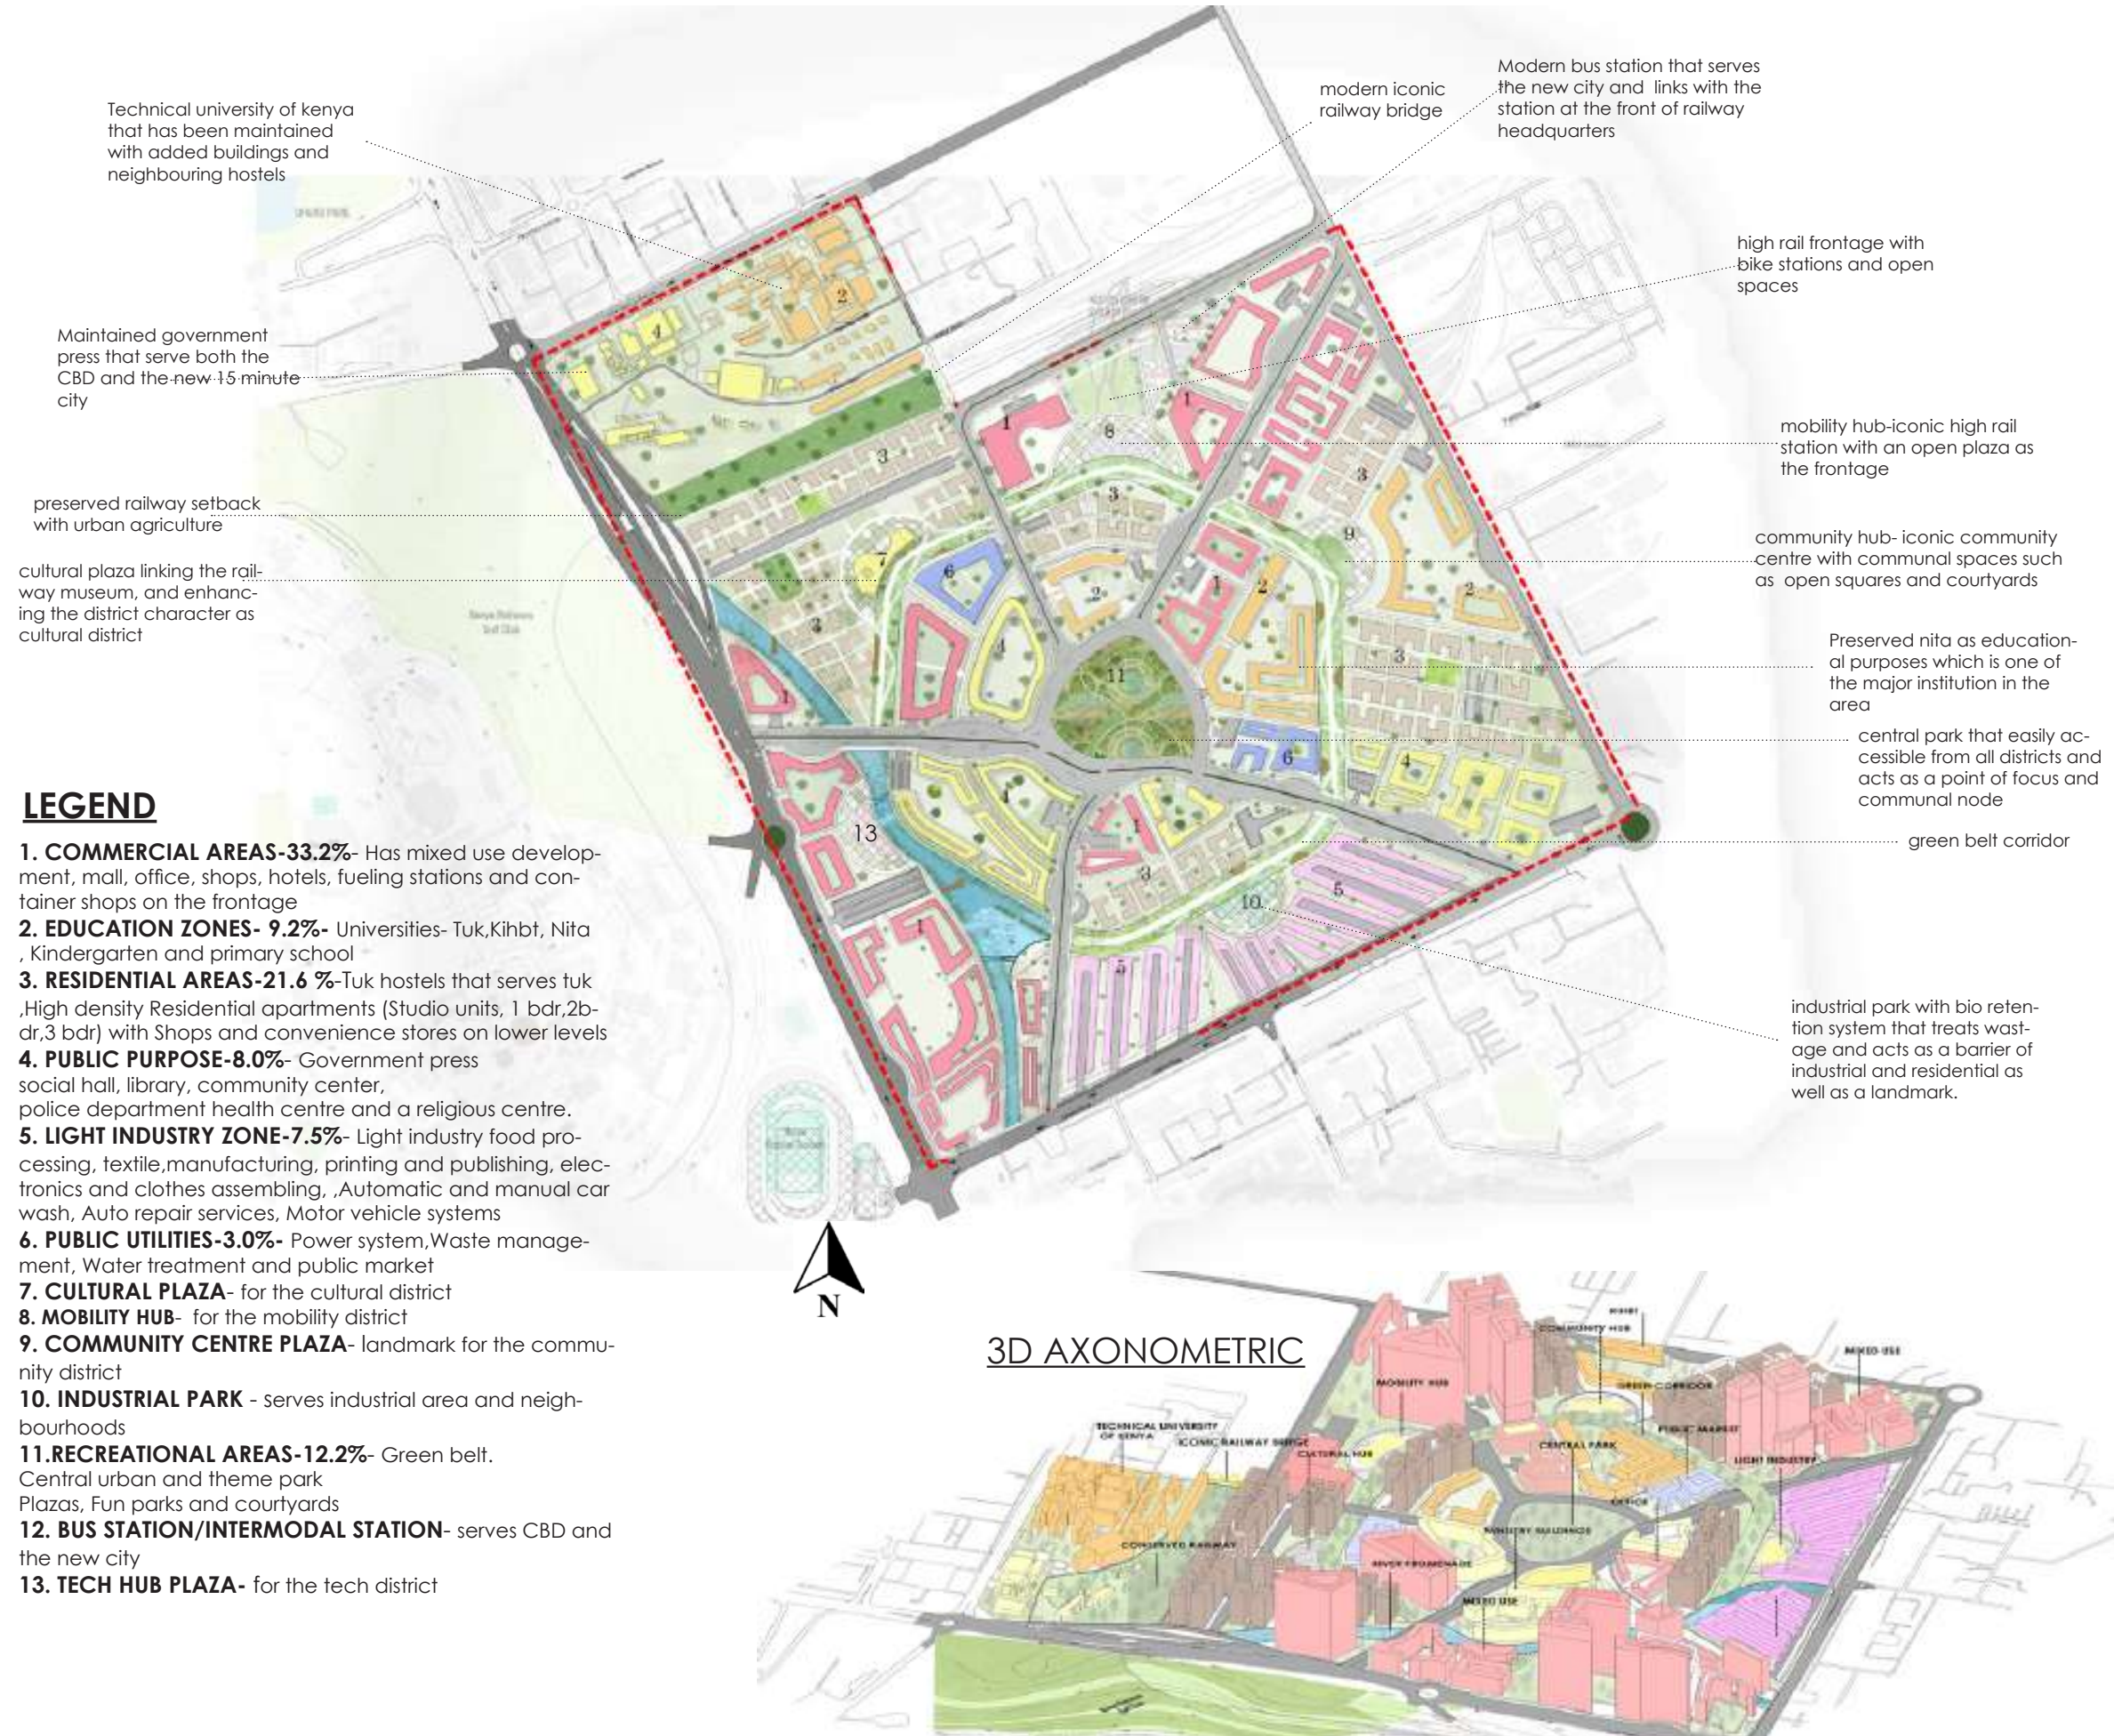

STREET ELEVATION SHOWING 15 MINUTE CONCEPT AMENITIES




STREETSCAPE OF VARIOUS PLAZAS




15 MINUTE CITY ANALYSIS - DISTRICT ANALYSIS

DISTRICT 2- 'MOBILITY DISTRICT' WITH MOBILITY HUB
HIGH SPEED RAIL STATION
COMMON PARKING
AMENITIES- SCHOOL,
AND MIXED FUNCTIONS

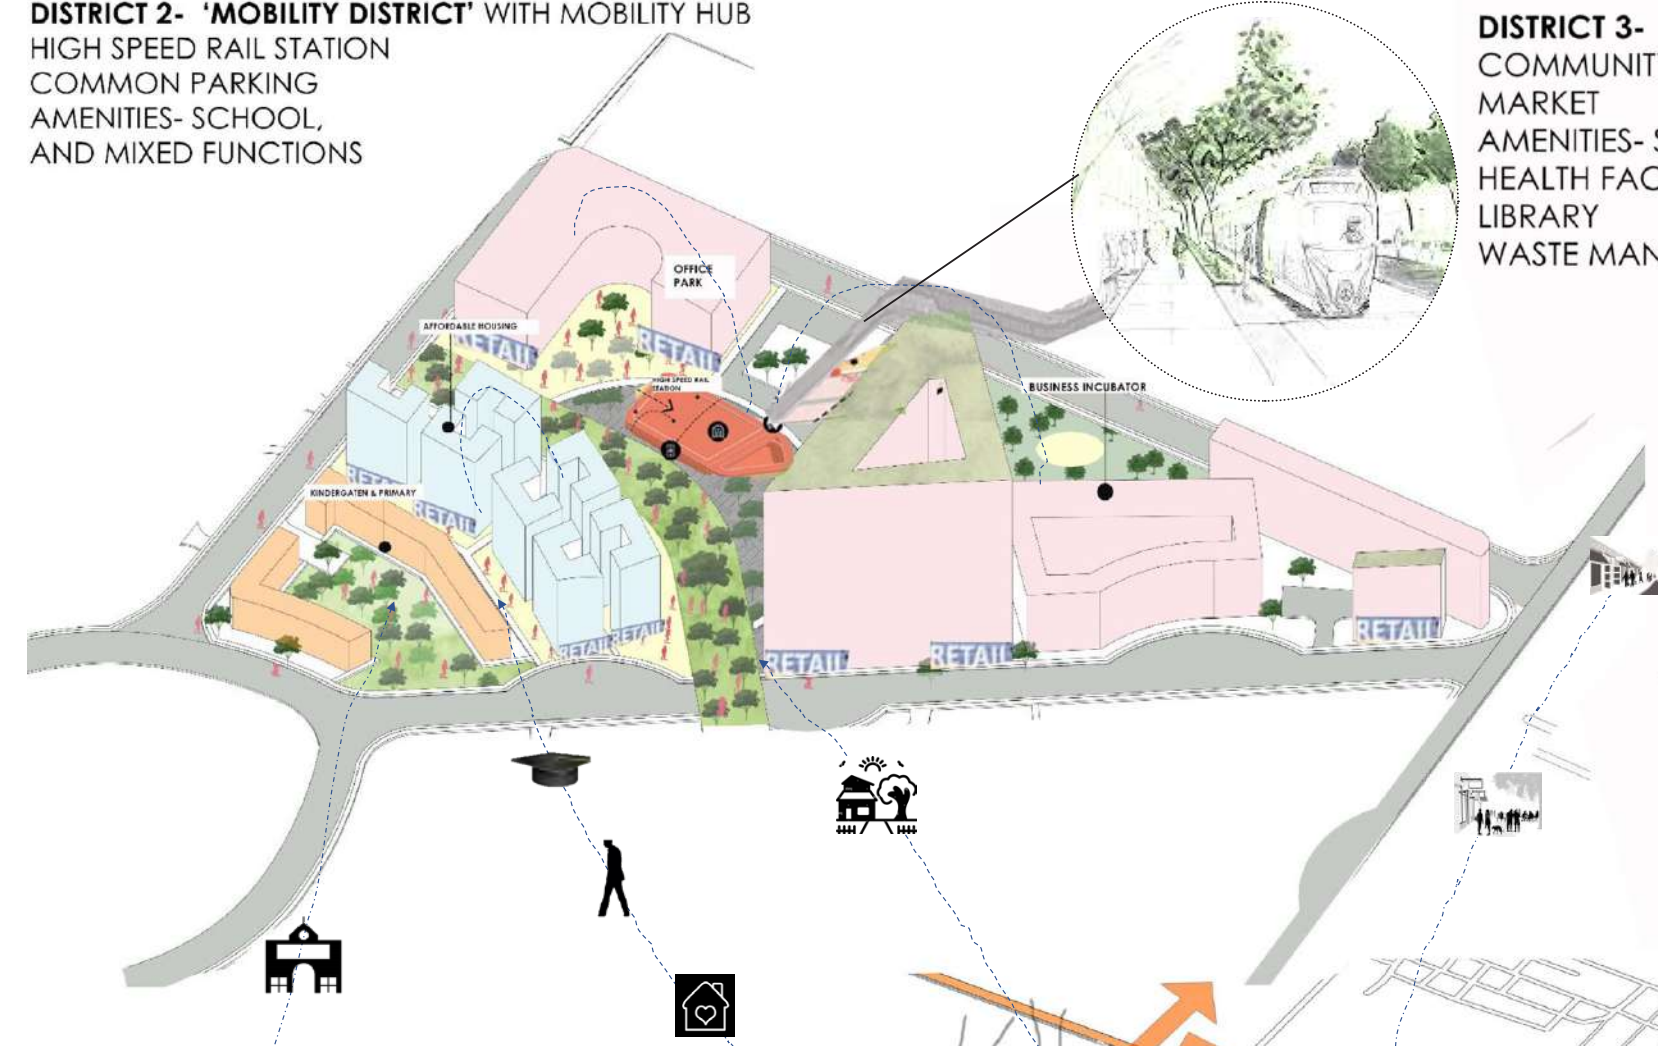


DISTRICT 3- 'COMMUNITY DISTRICT' WITH COMMUNITY HUB
COMMUNITY CENTRE
MARKET
AMENITIES- SCHOOL,
HEALTH FACILITY
LIBRARY
WASTE MANAGEMENT

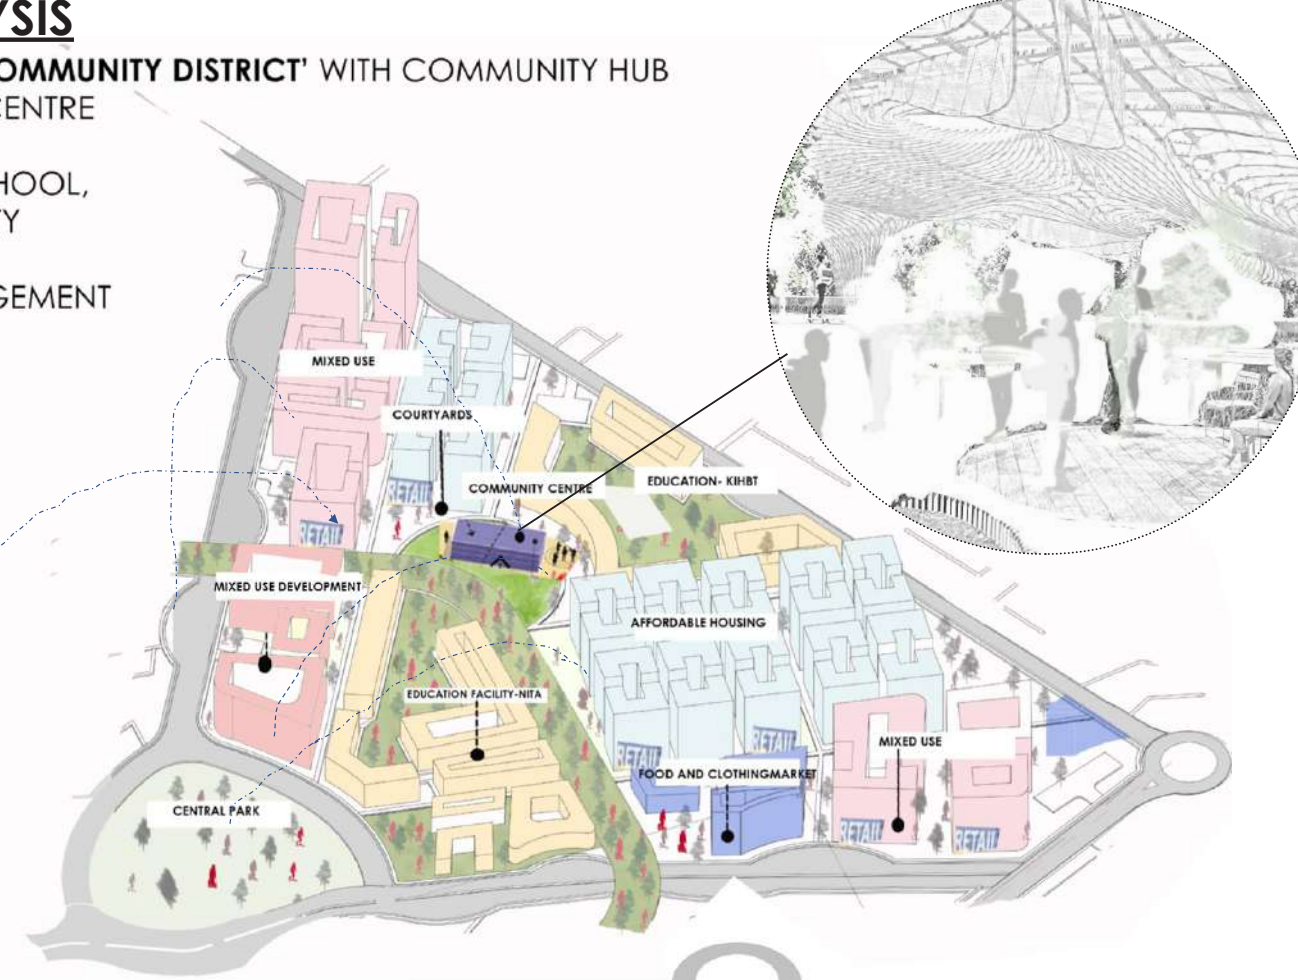

DISTRICT 1- 'CULTURAL DISTRICT' WITH CULTURAL LANDMARK
1.RAILWAY MUSEUM
2.URBAN AGRICULTURE,
3.AMENITIES- SCHOOL,
4.POLICE STATION, POWER STATION




DISTRICT 5 'OFFICE BUSINESS DISTRICT'
1.OFFICES
2. MINISTRY BUILDINGS
3. RE=IVER PROMENADE

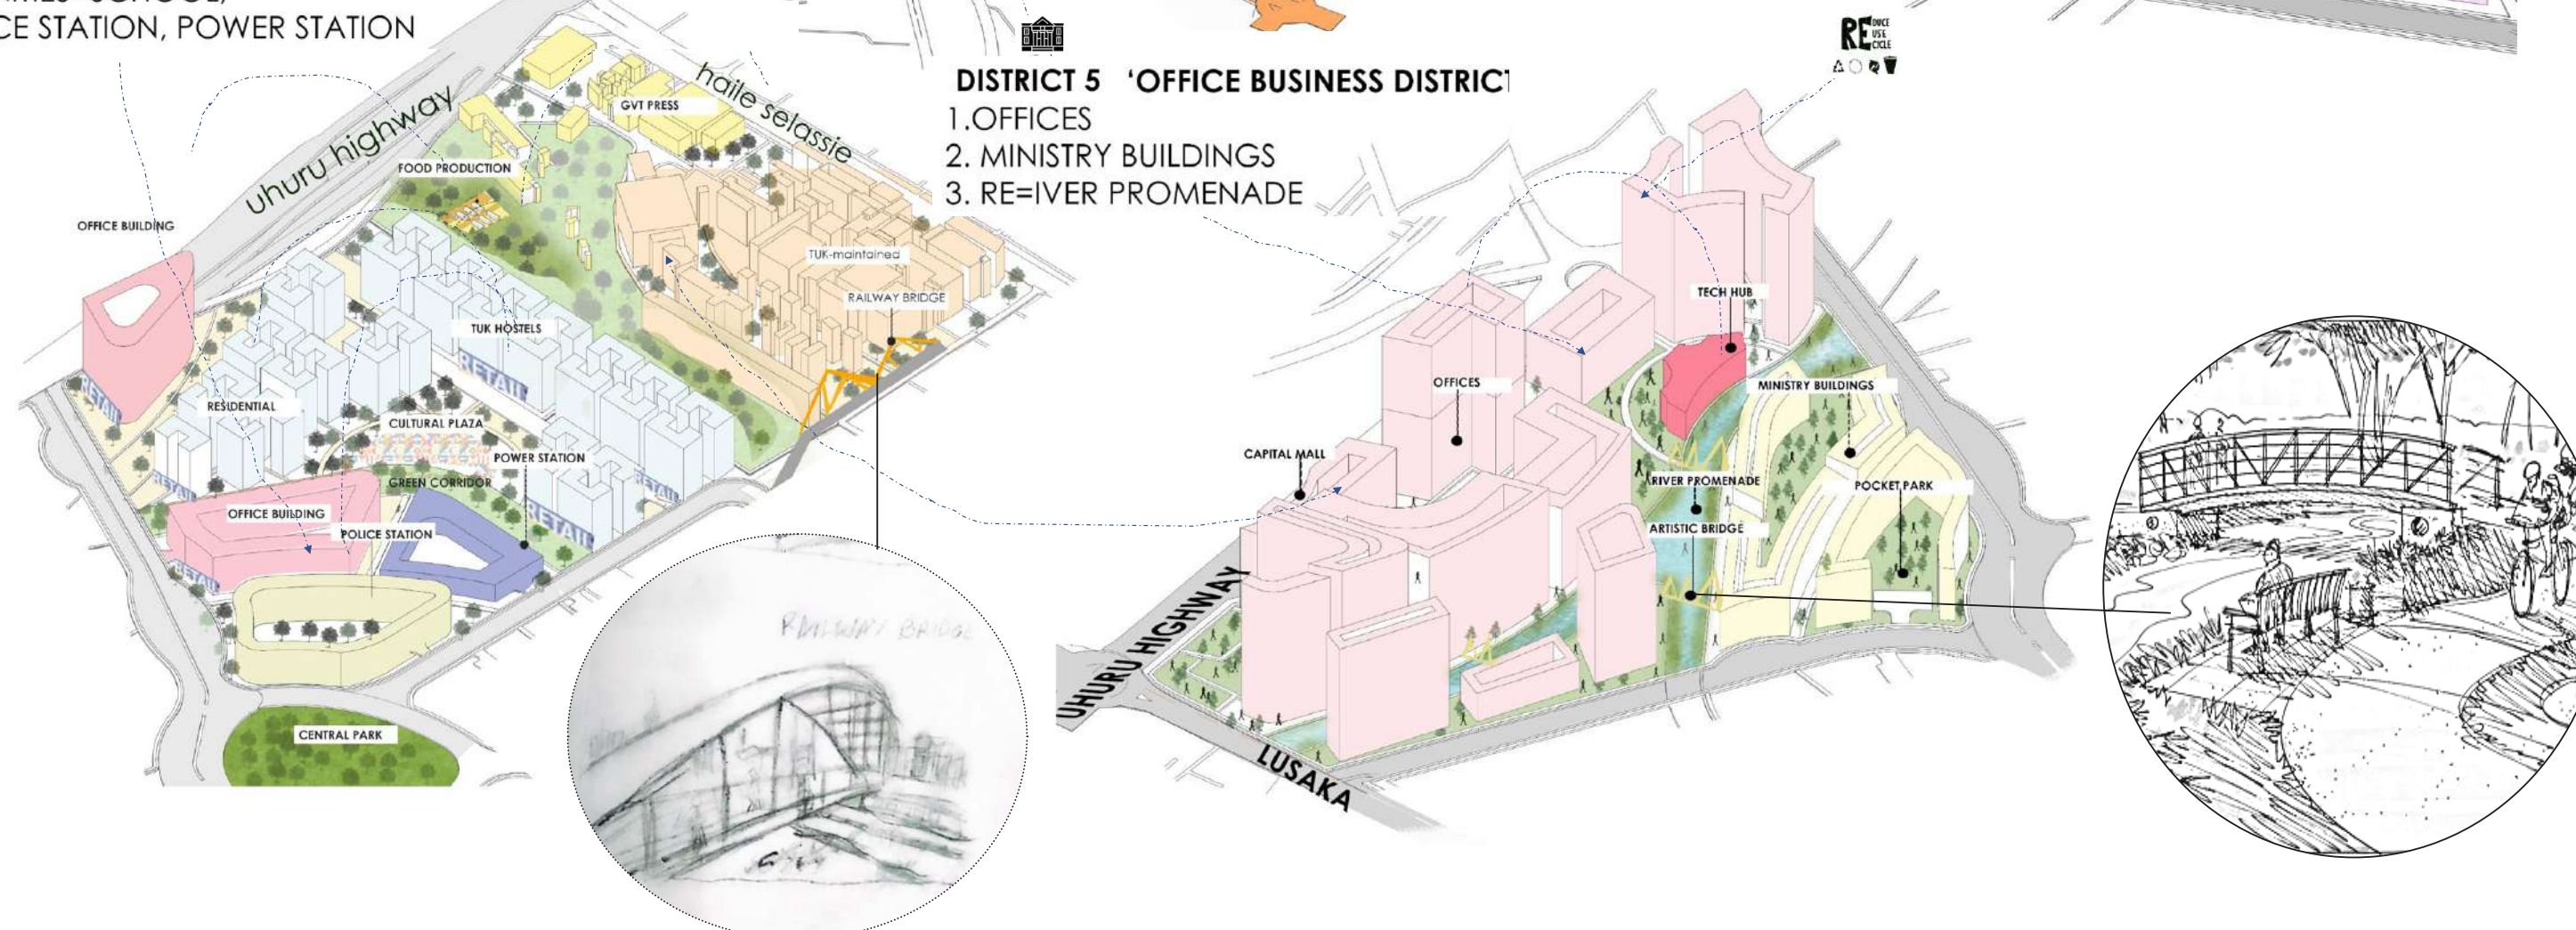




MIXED USE BUILDING DESIGN

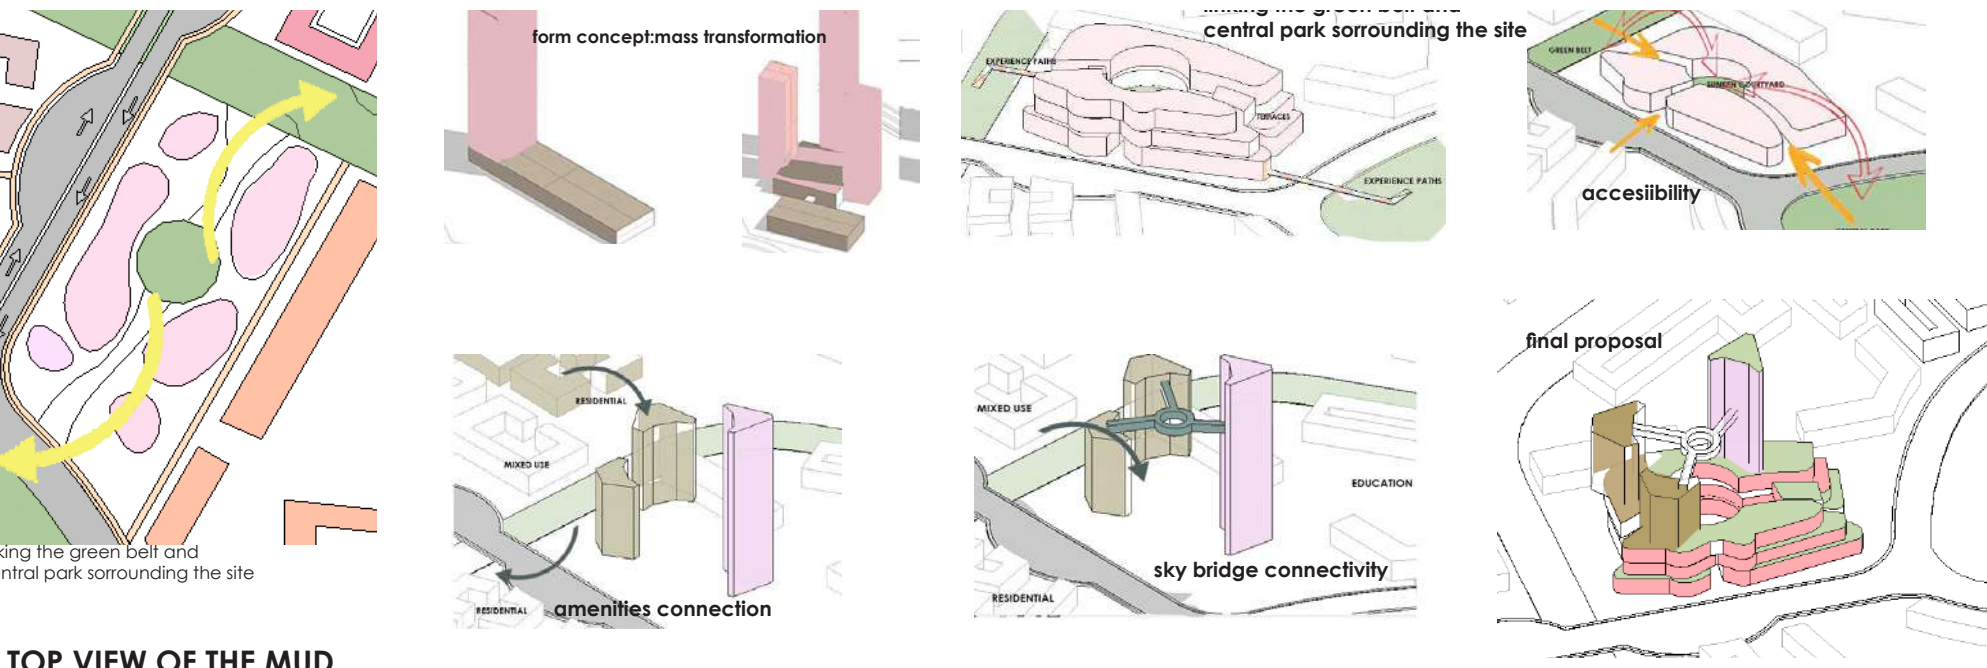

TOP VIEW OF THE MUD

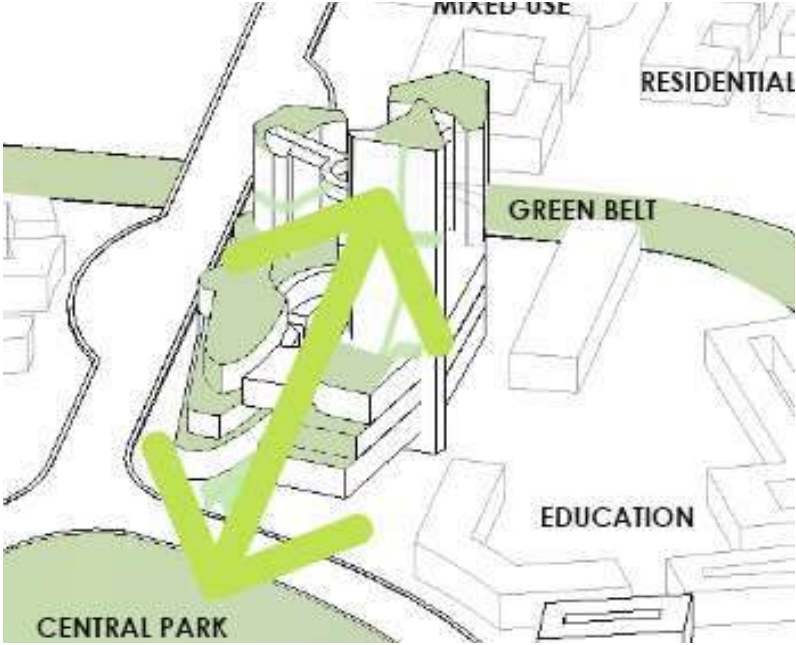

URBAN CONNECTIVITY AND BREATHABLE ENVELOPE

Connecting the green spaces and introduction of green space in the middle of the project. The building is designed in a controlled way to create a breathable envelope. There is use of sunken courtyard, open corridor terraces.

3D VIEW SHOWING ENTRANCE



GROUND FLOOR PLAN



skating continuation from the green belt
throughout the mixed use development
and through the experience paths



sketch of sunken courtyard viewed from ground floor with seating spaces, green areas and accessible kiosks inside the basements




Bicycle parking at the front of the mixed use development, which is accessible directly from the main road and the main entrance, the people can cycle throughout





BASEMENT 2

Has retail shops around the central sunken courtyard (which has seating spces, landscaped lawns and children play area) and the basement has ramps accessing basement 2 from the central courtyard

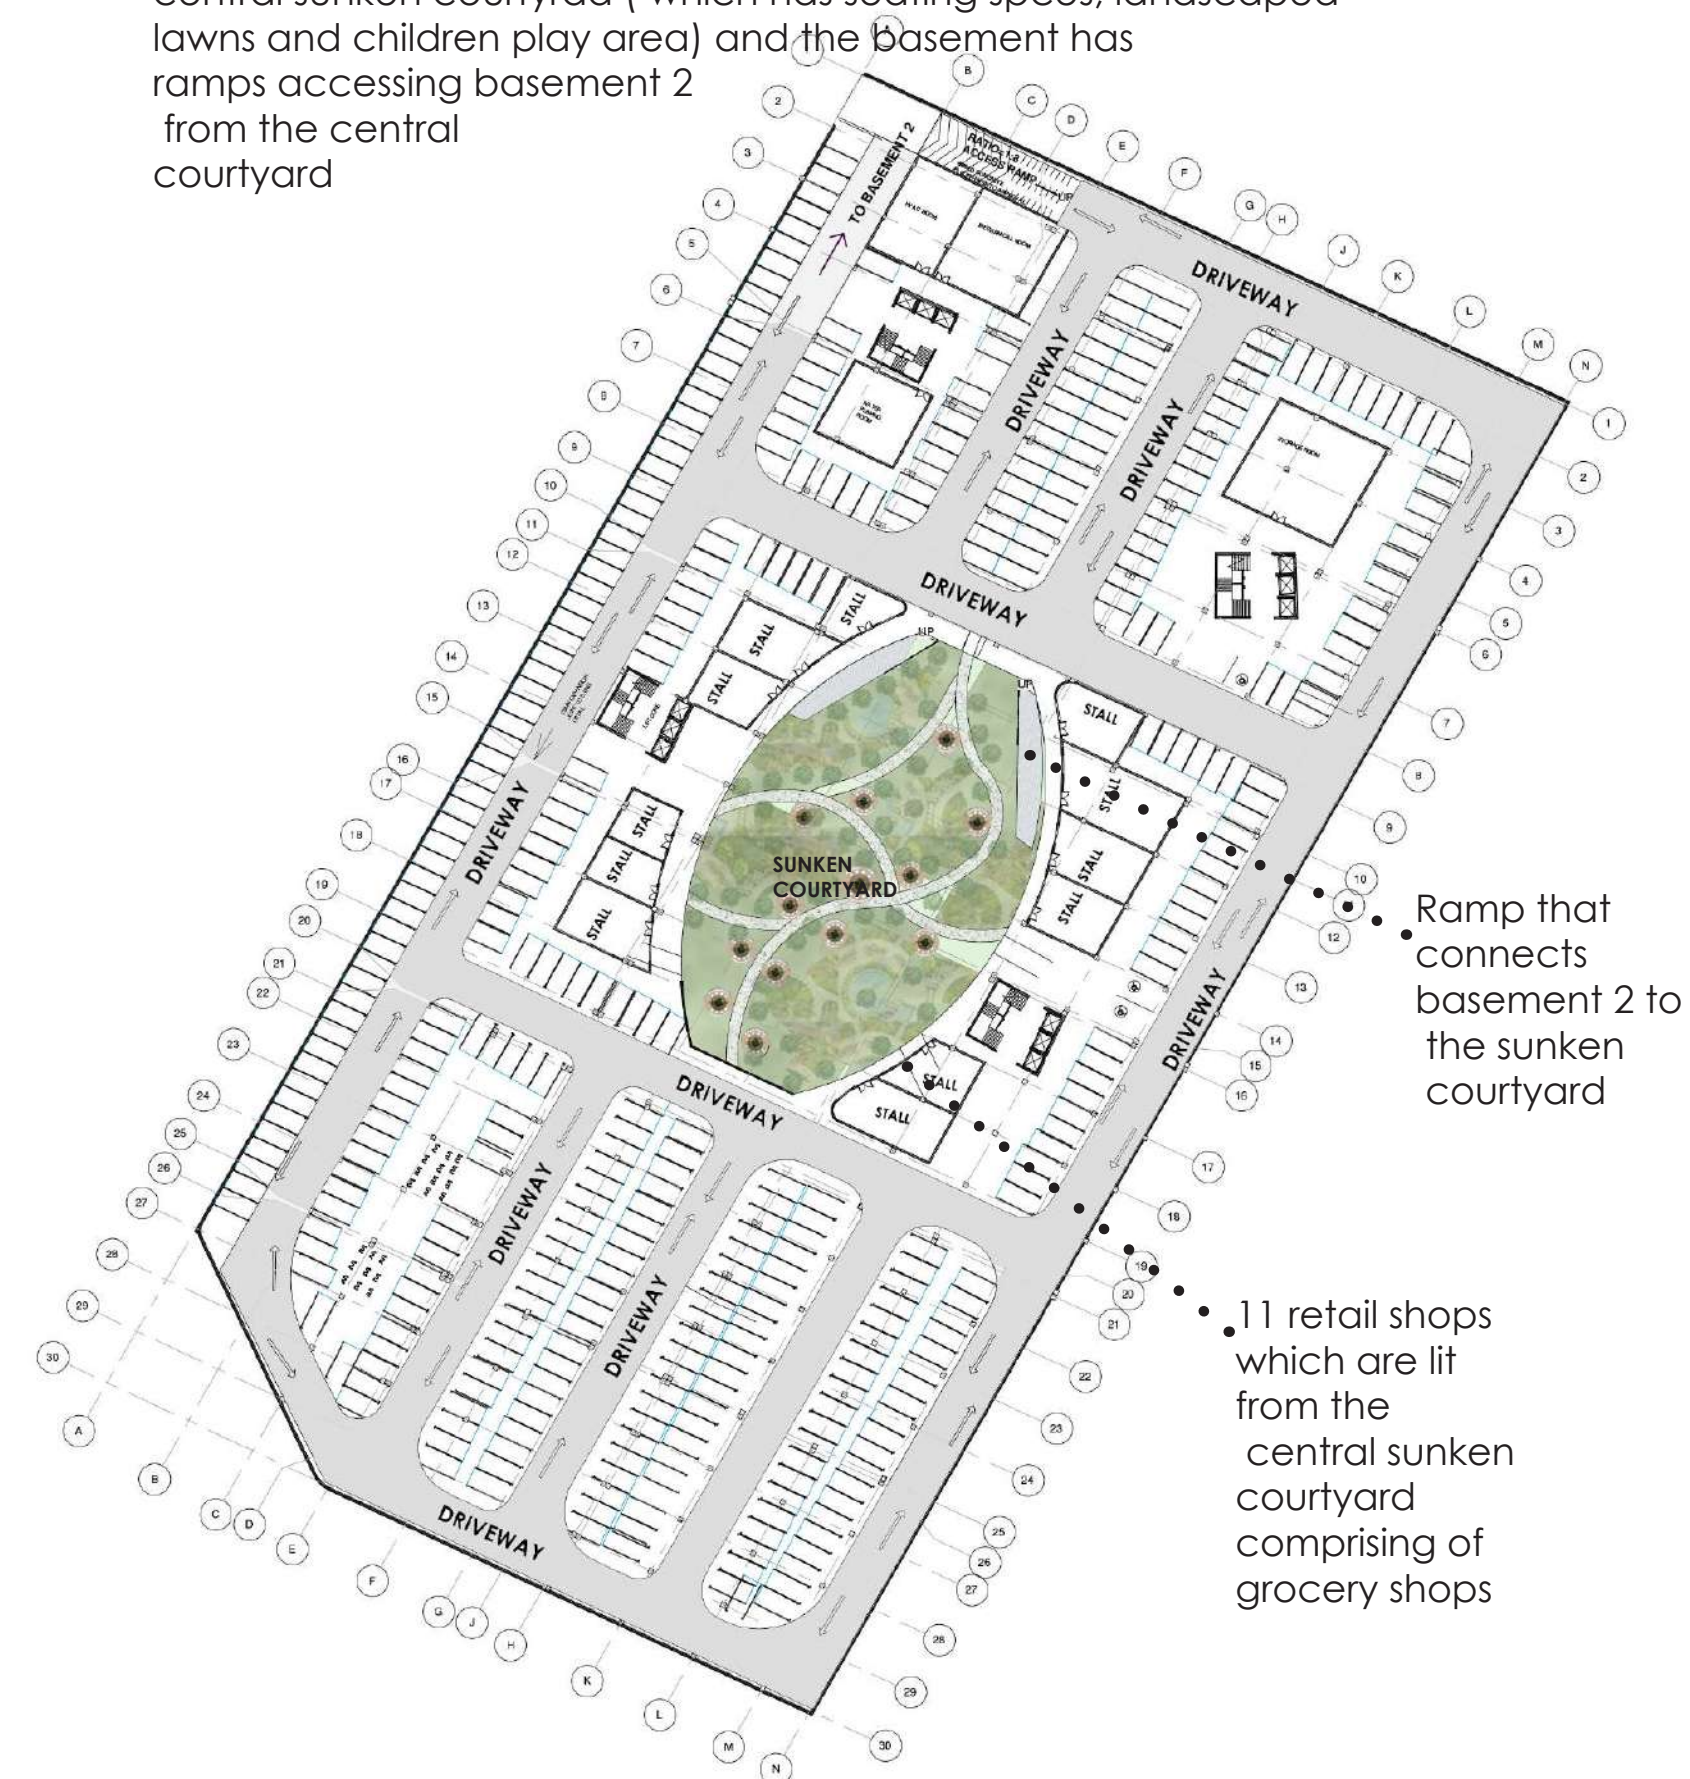


- Ramp that connects basement 2 to the sunken courtyard

- 11 retail shops which are lit from the central sunken courtyard comprising of grocery shops

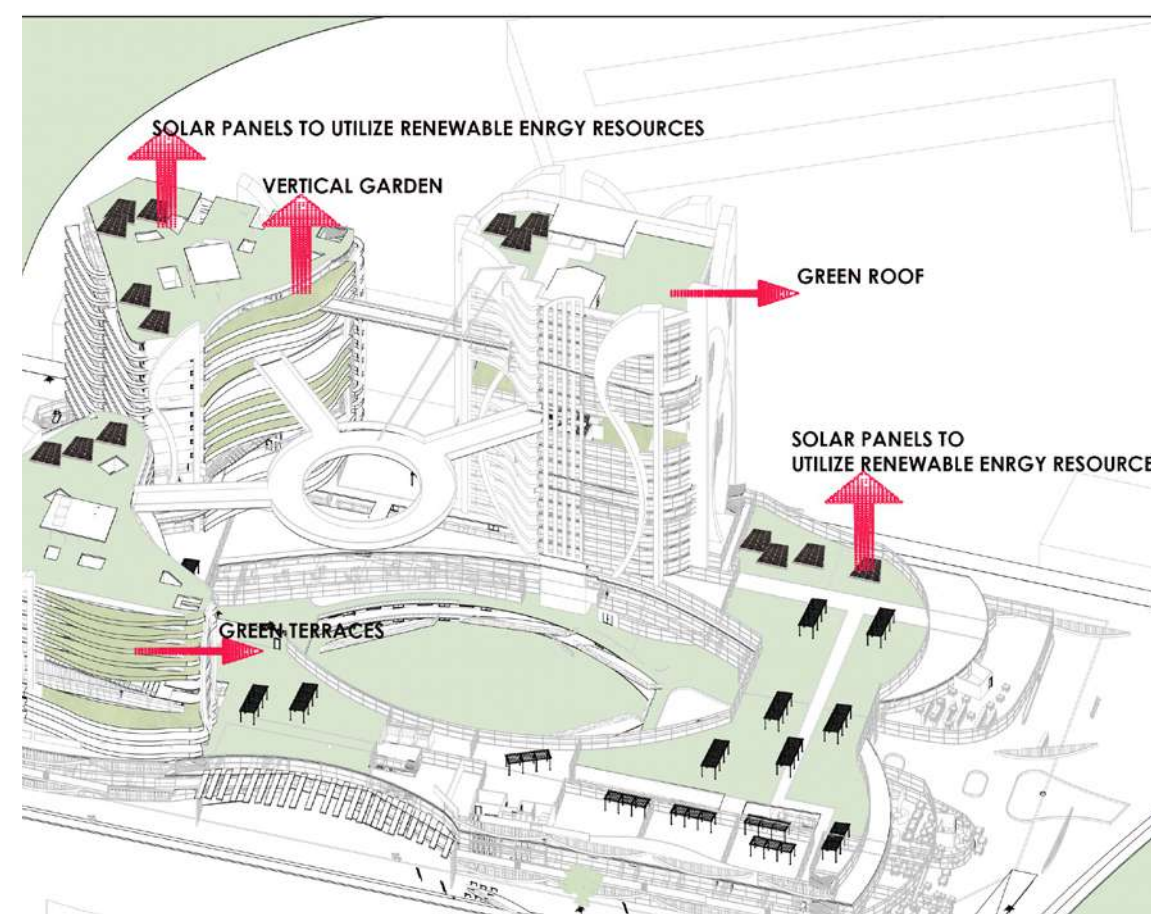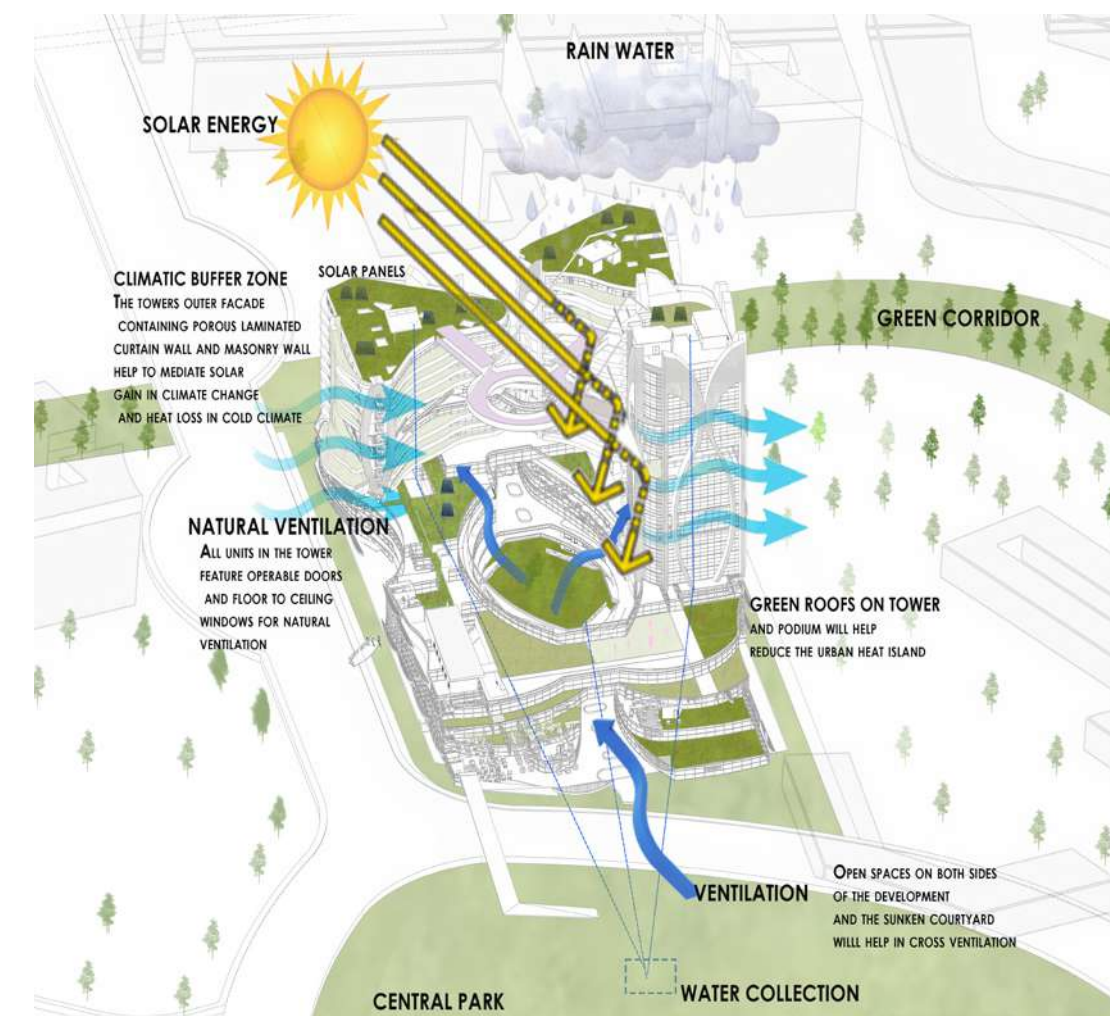


FIRST FLOOR

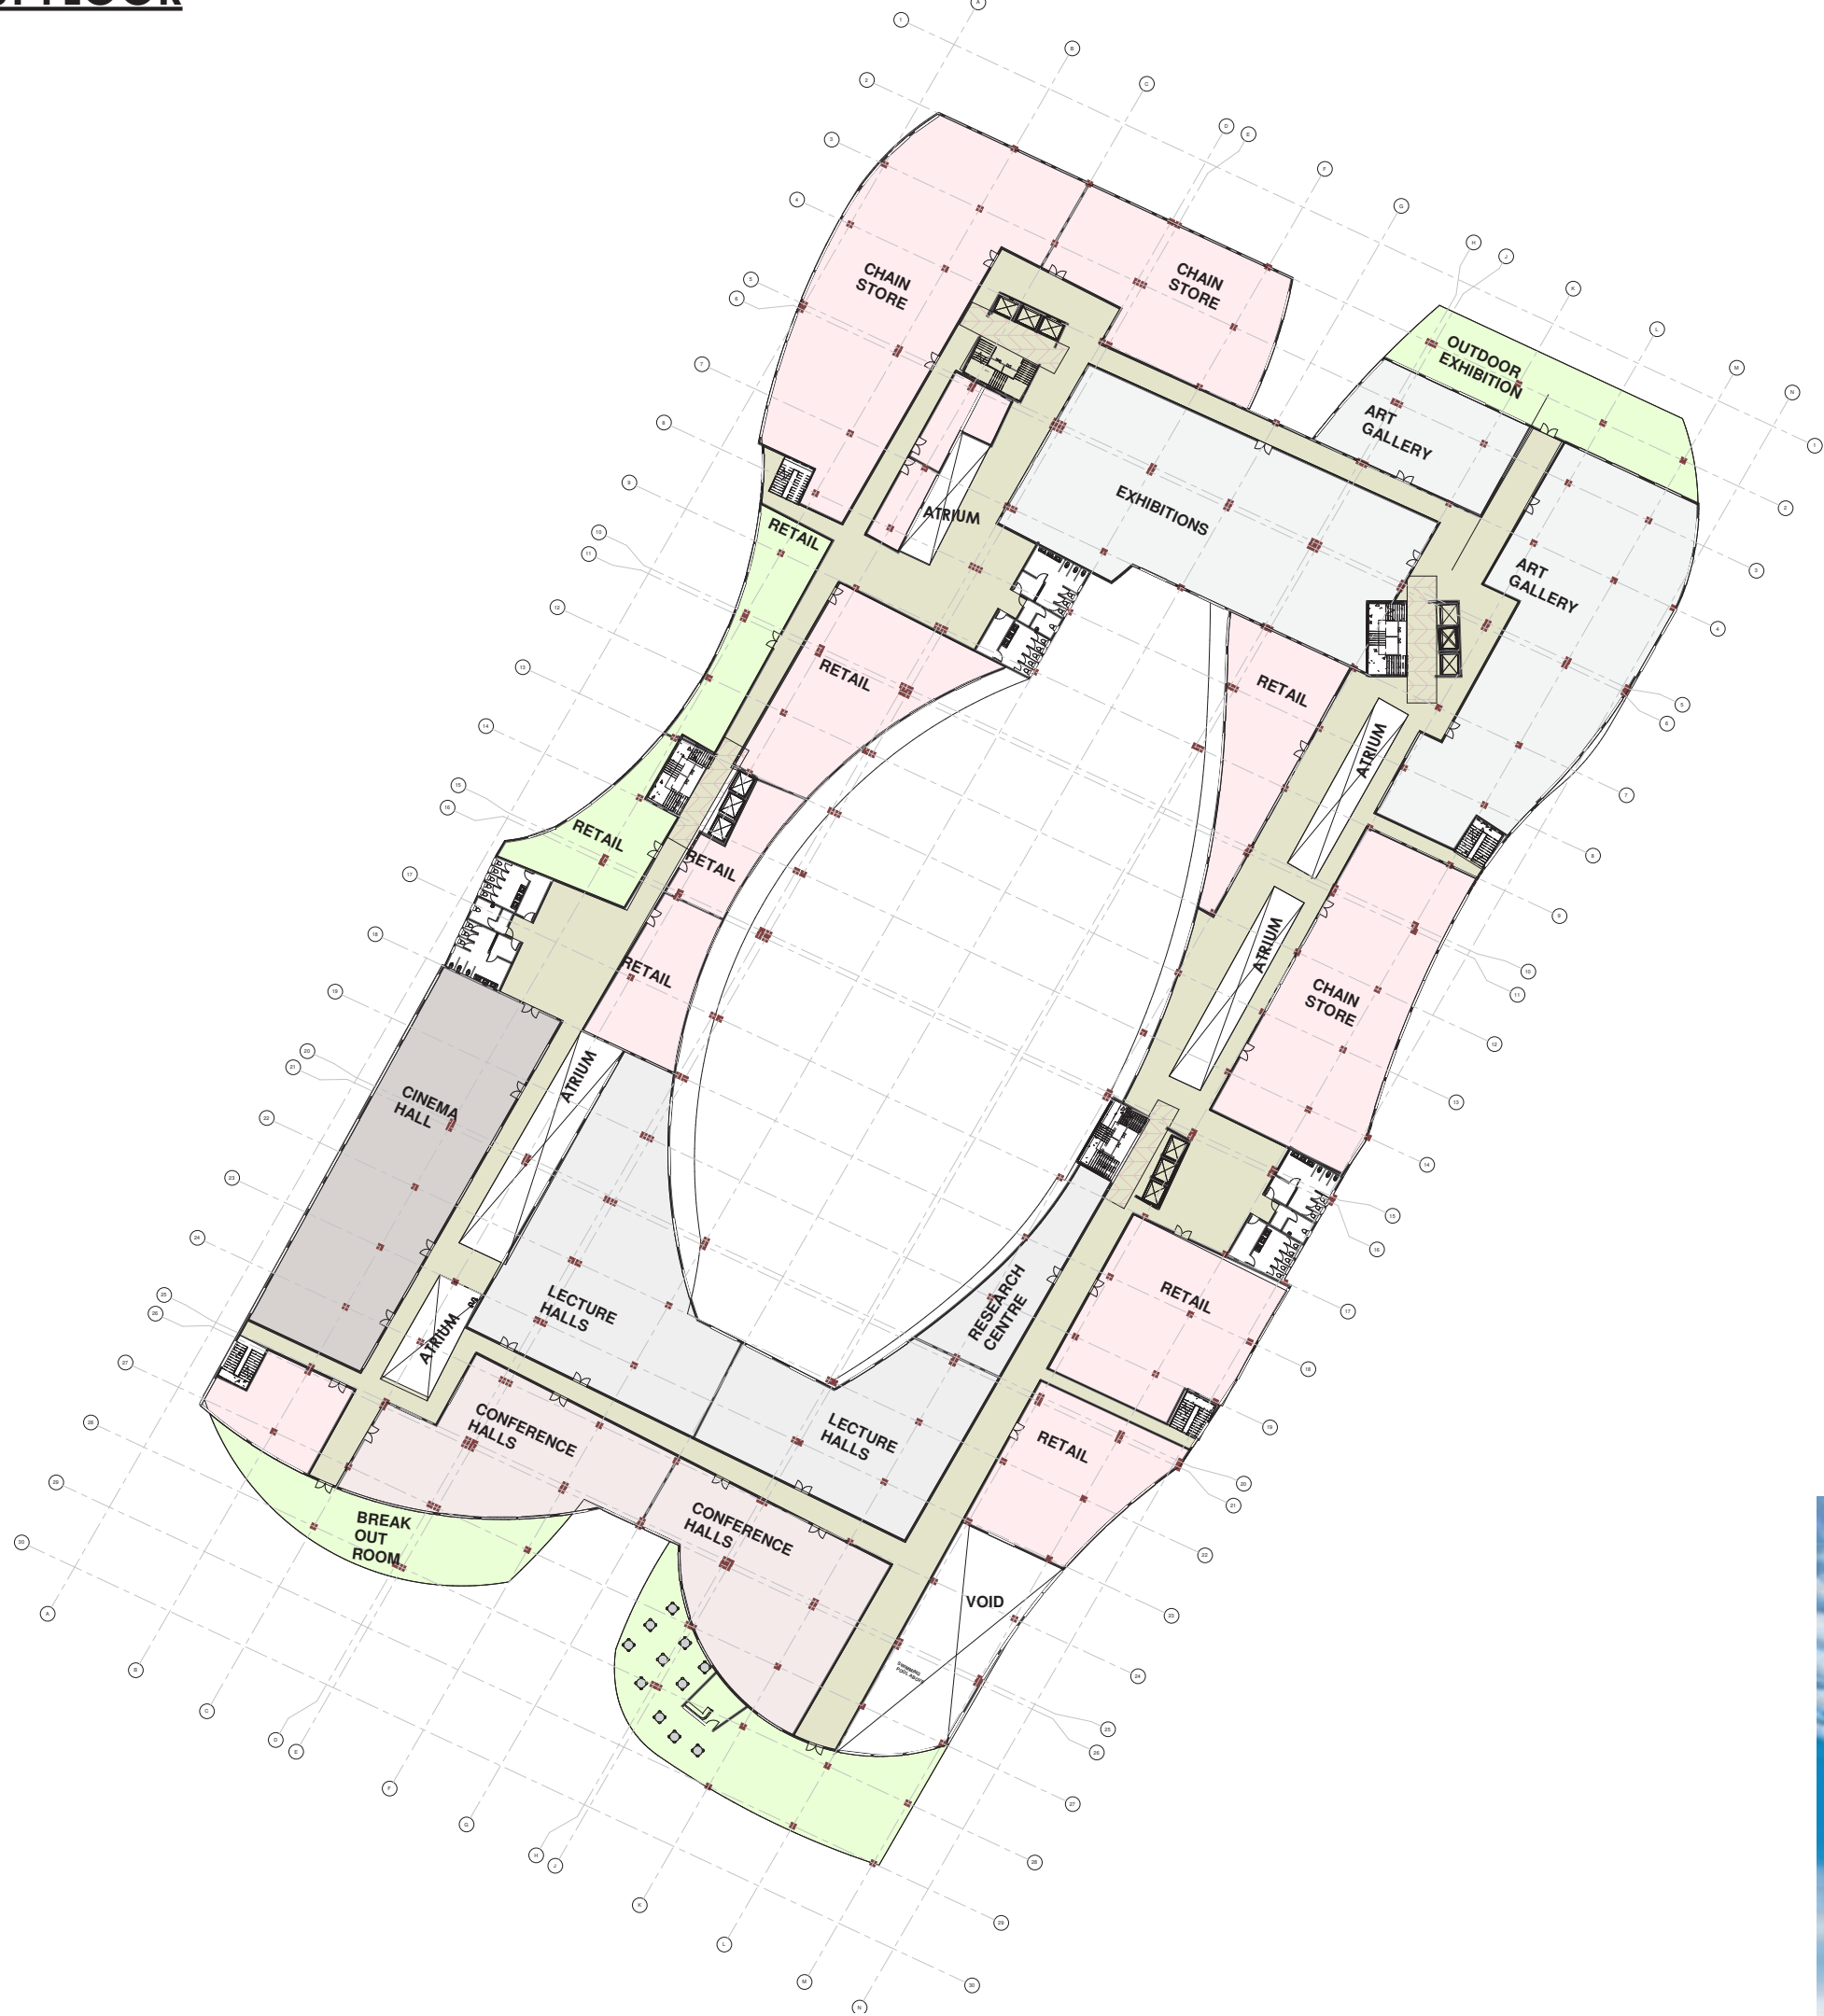


RESIDENTIAL FLOORS




FRONT ELEVATION.

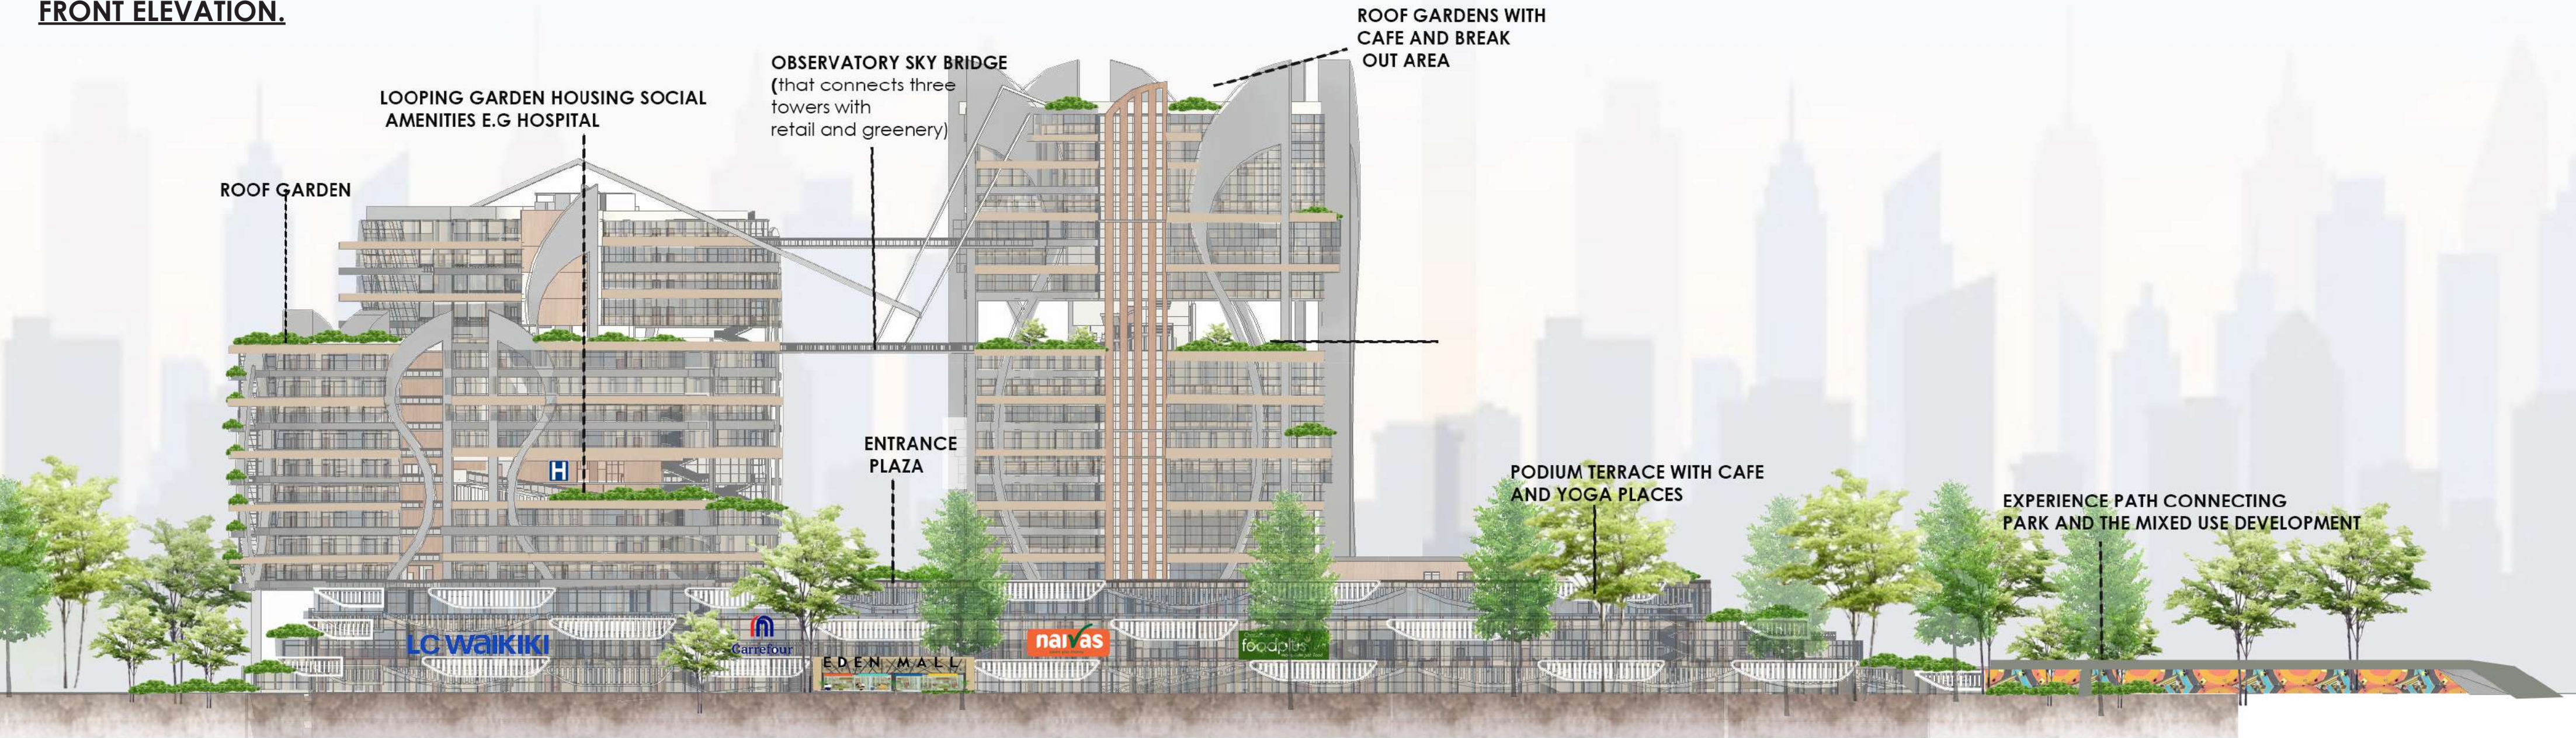


SECTION SHOWING CIRCULATION

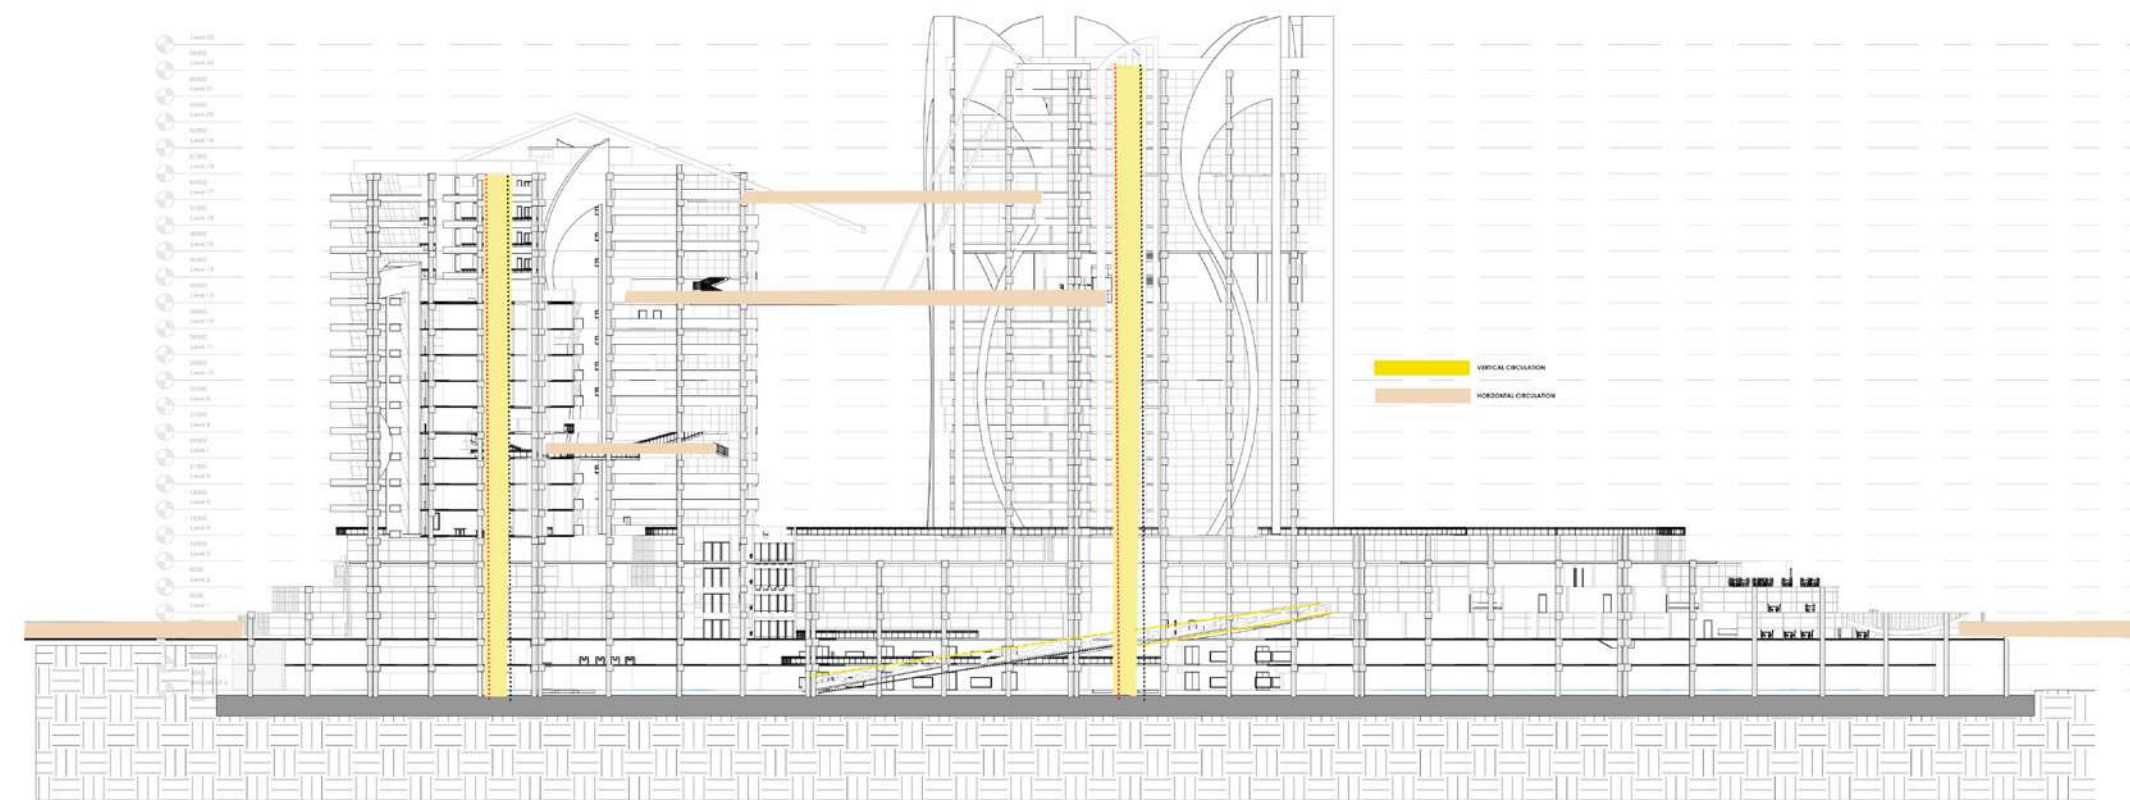


AMENITIES SECTION

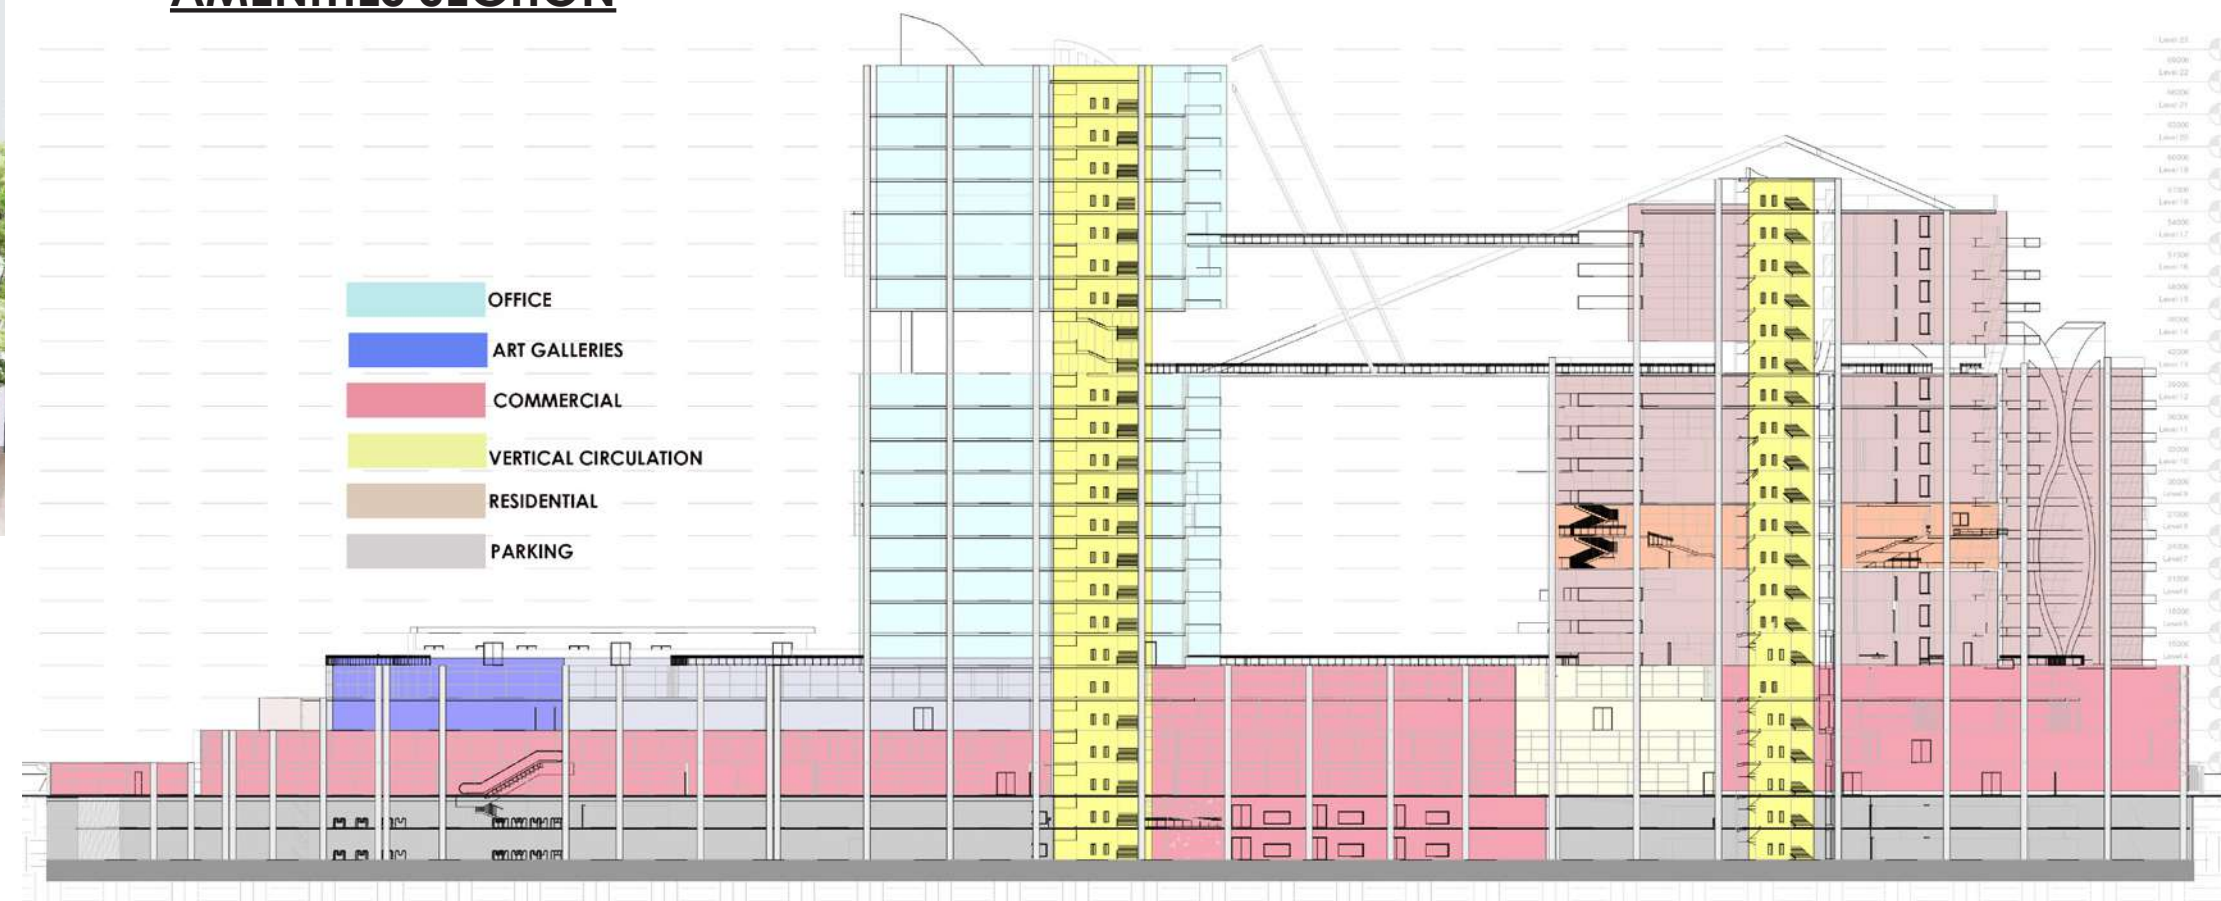


EAST ELEVATION

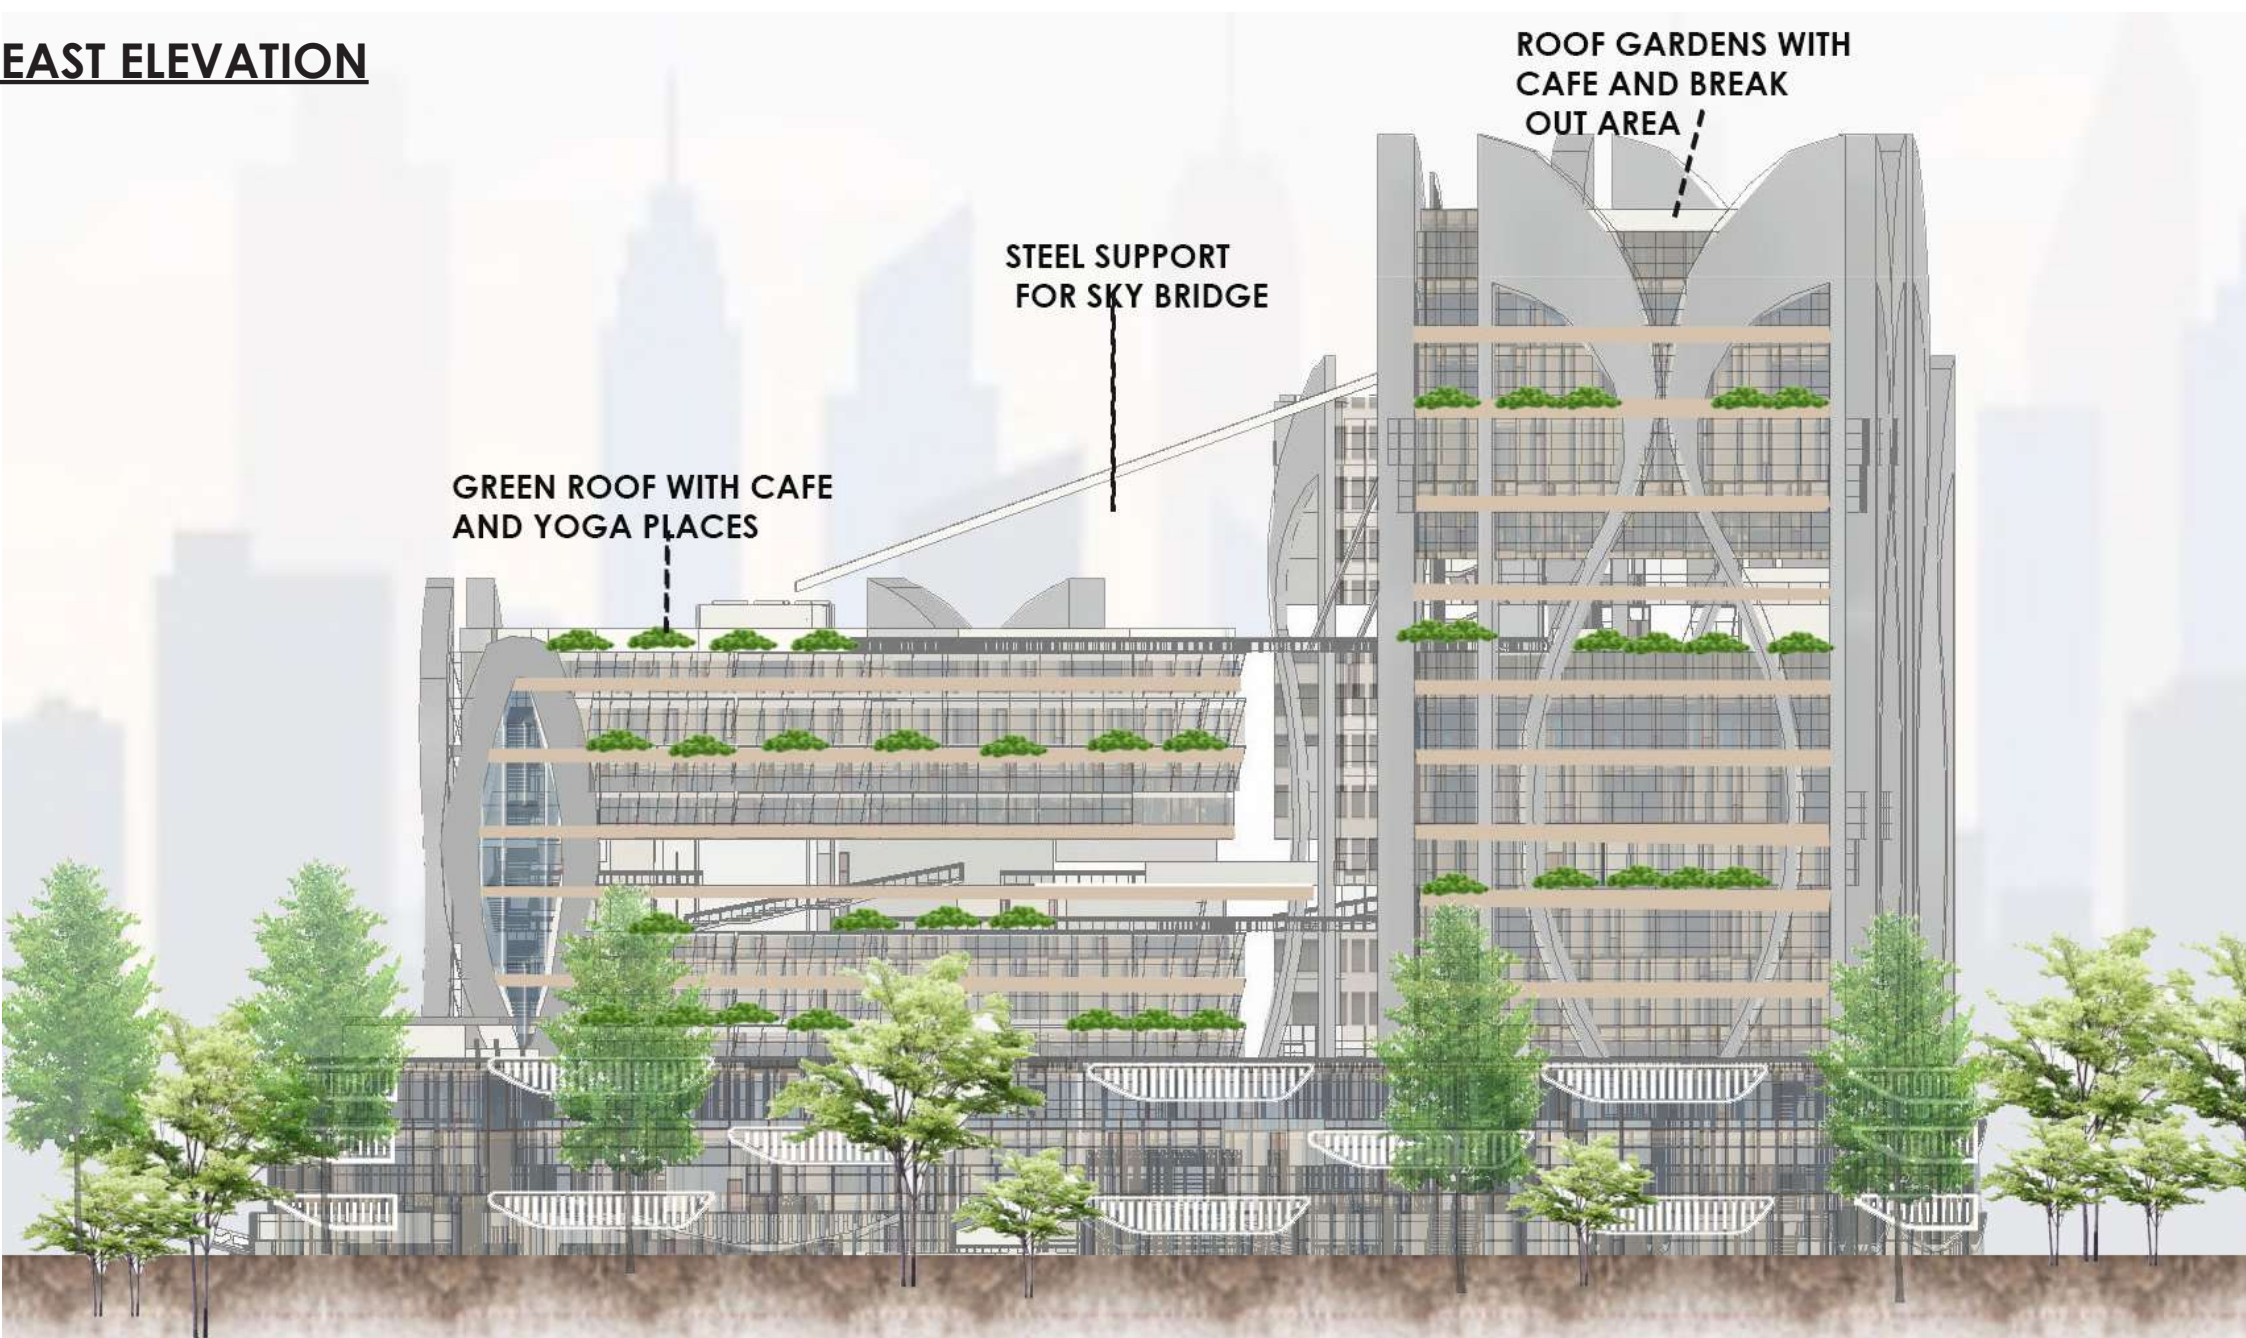

02 AFFORDABLE HOUSING

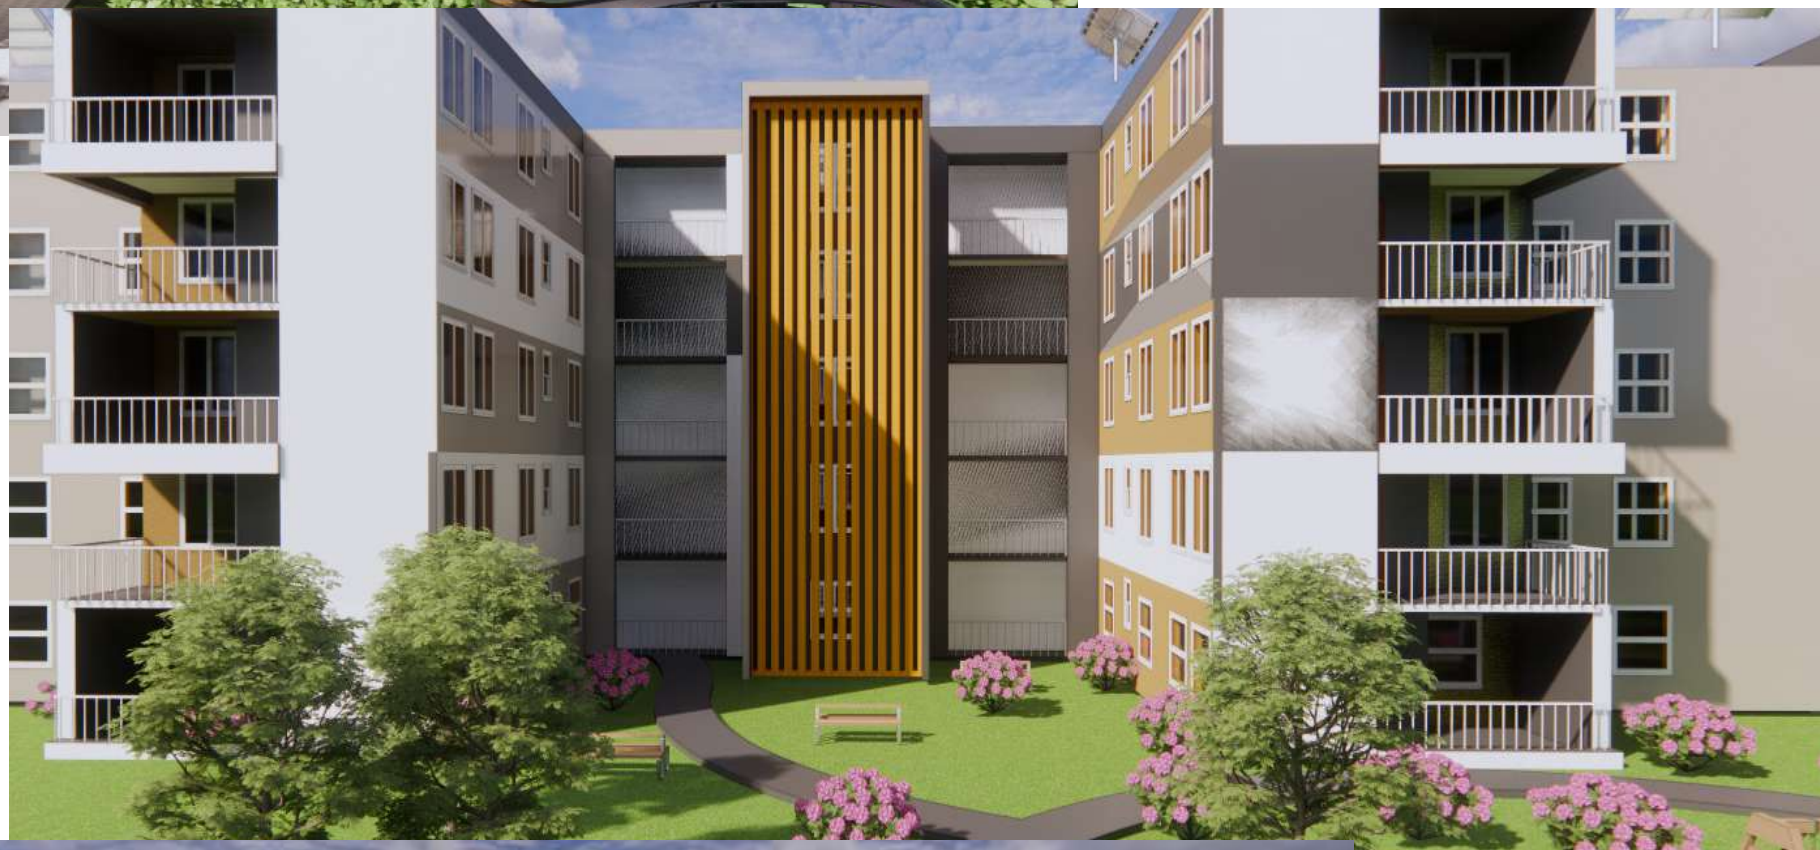


AXONOMETRIC PROJECTION

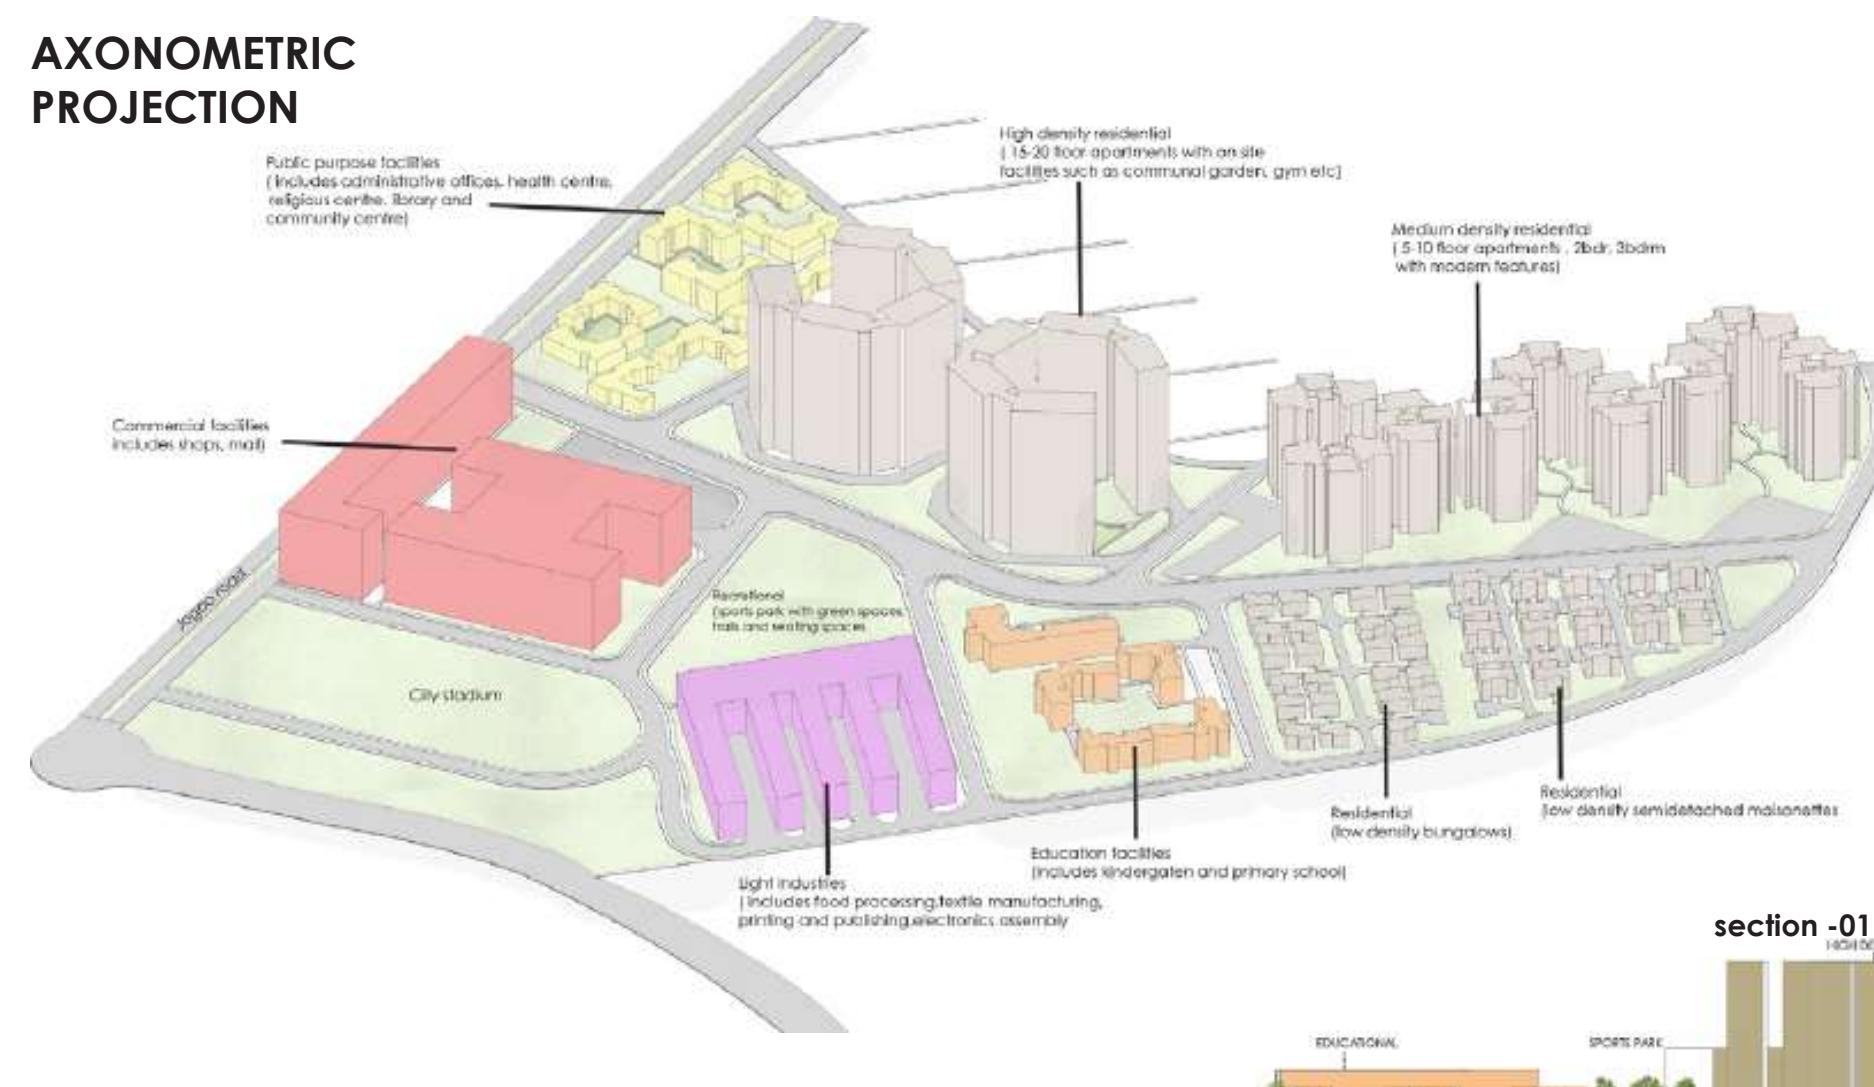

CLUSTER PLAN




UNIT PLAN

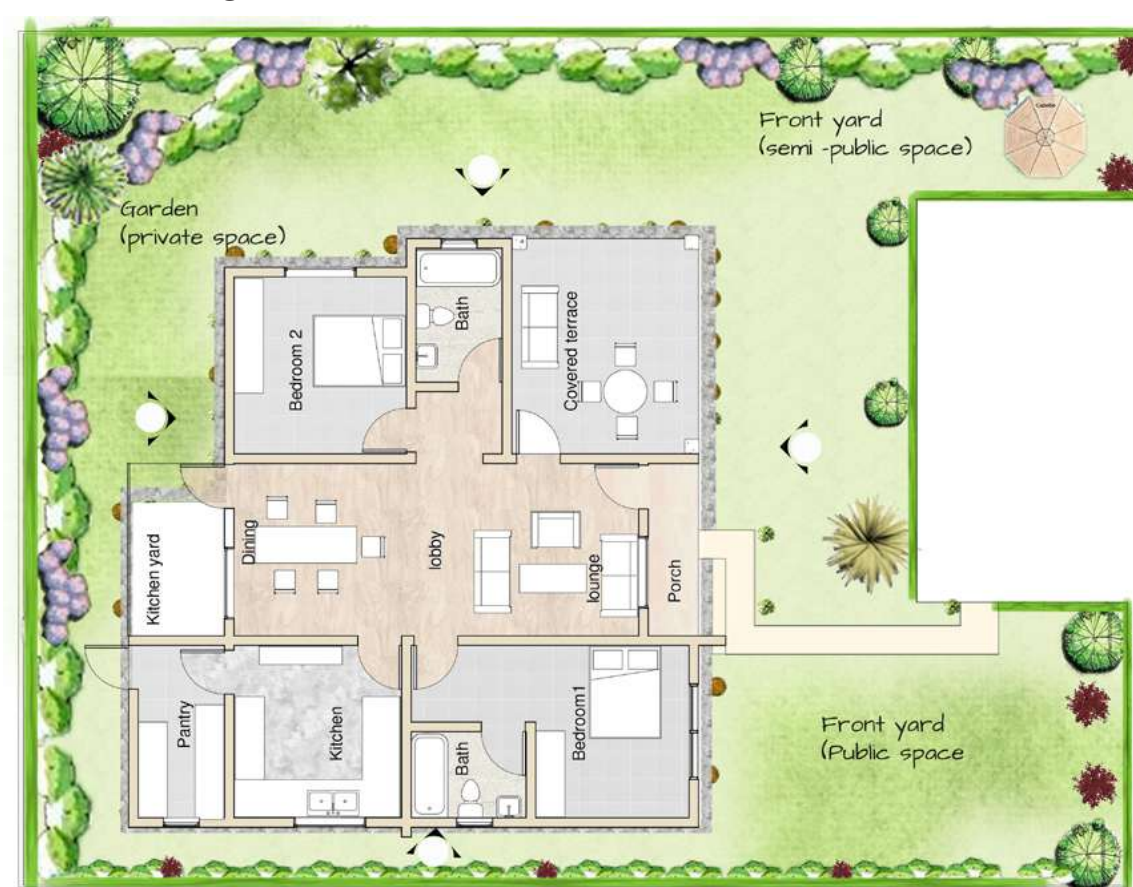

INCREMENTAL TRANSFORMATION
UNIT PLAN AFTER TRANSFORMATION(extra bedroom)
making it a three bedroom bungalow

constructed using high density asphalt.

**AFFORDABILITY CONCEPT:
SUBLETTING AND INCREMENTAL.**The owner can increase a room at the terrace and subdivide the bungalow into single rooms and sublet.

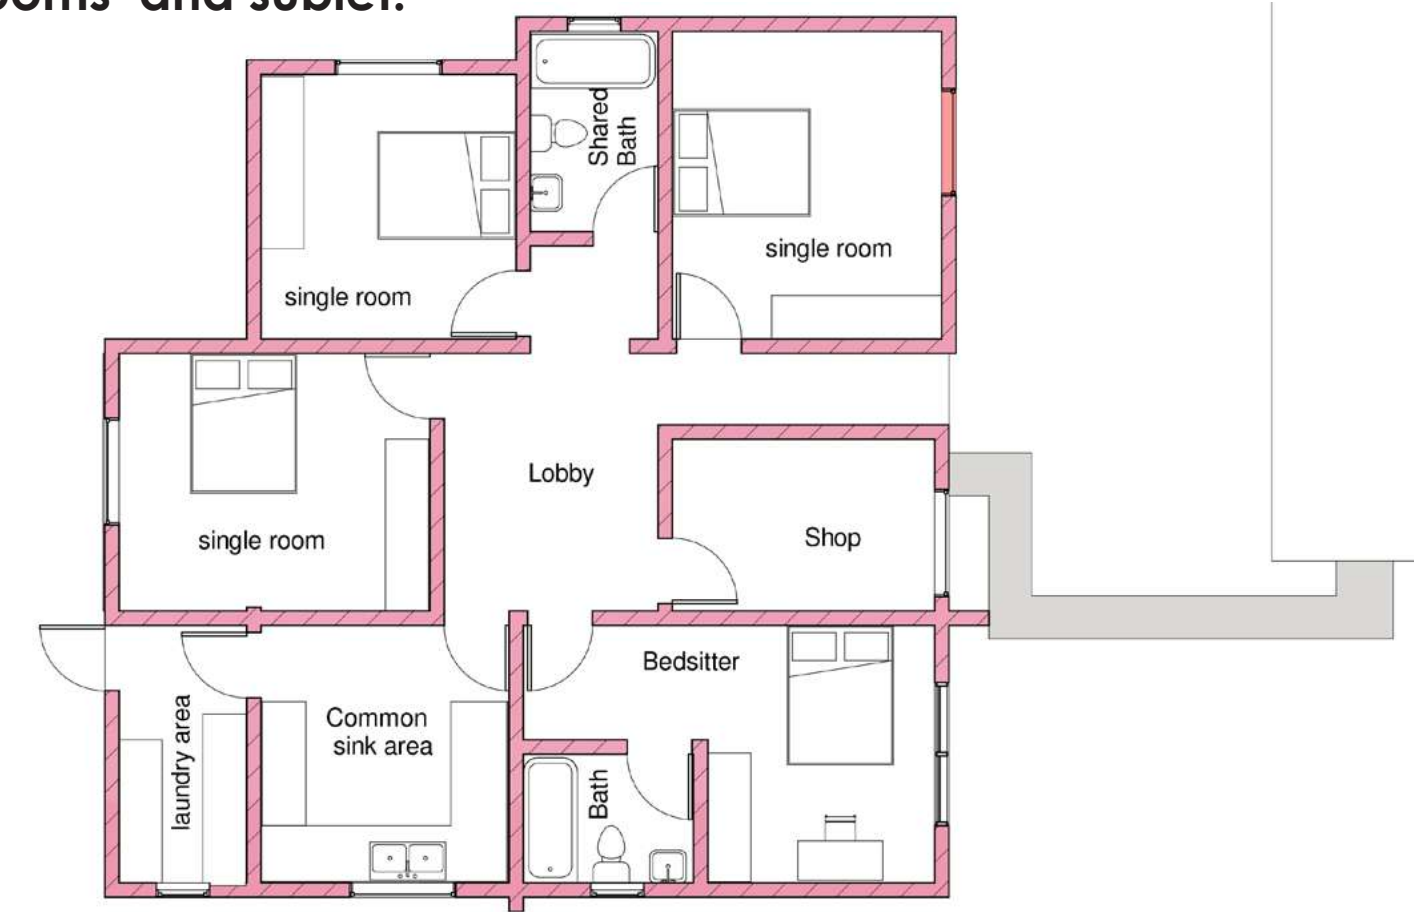

CLUSTER 3D RENDER

FRONT ELEVATION



BACK ELEVATION



CLUSTER 3D VIEW



MASTER PLAN



CLUSTER PLAN




CLUSTER ELEVATION



CLUSTER 3D



UNIT PLAN

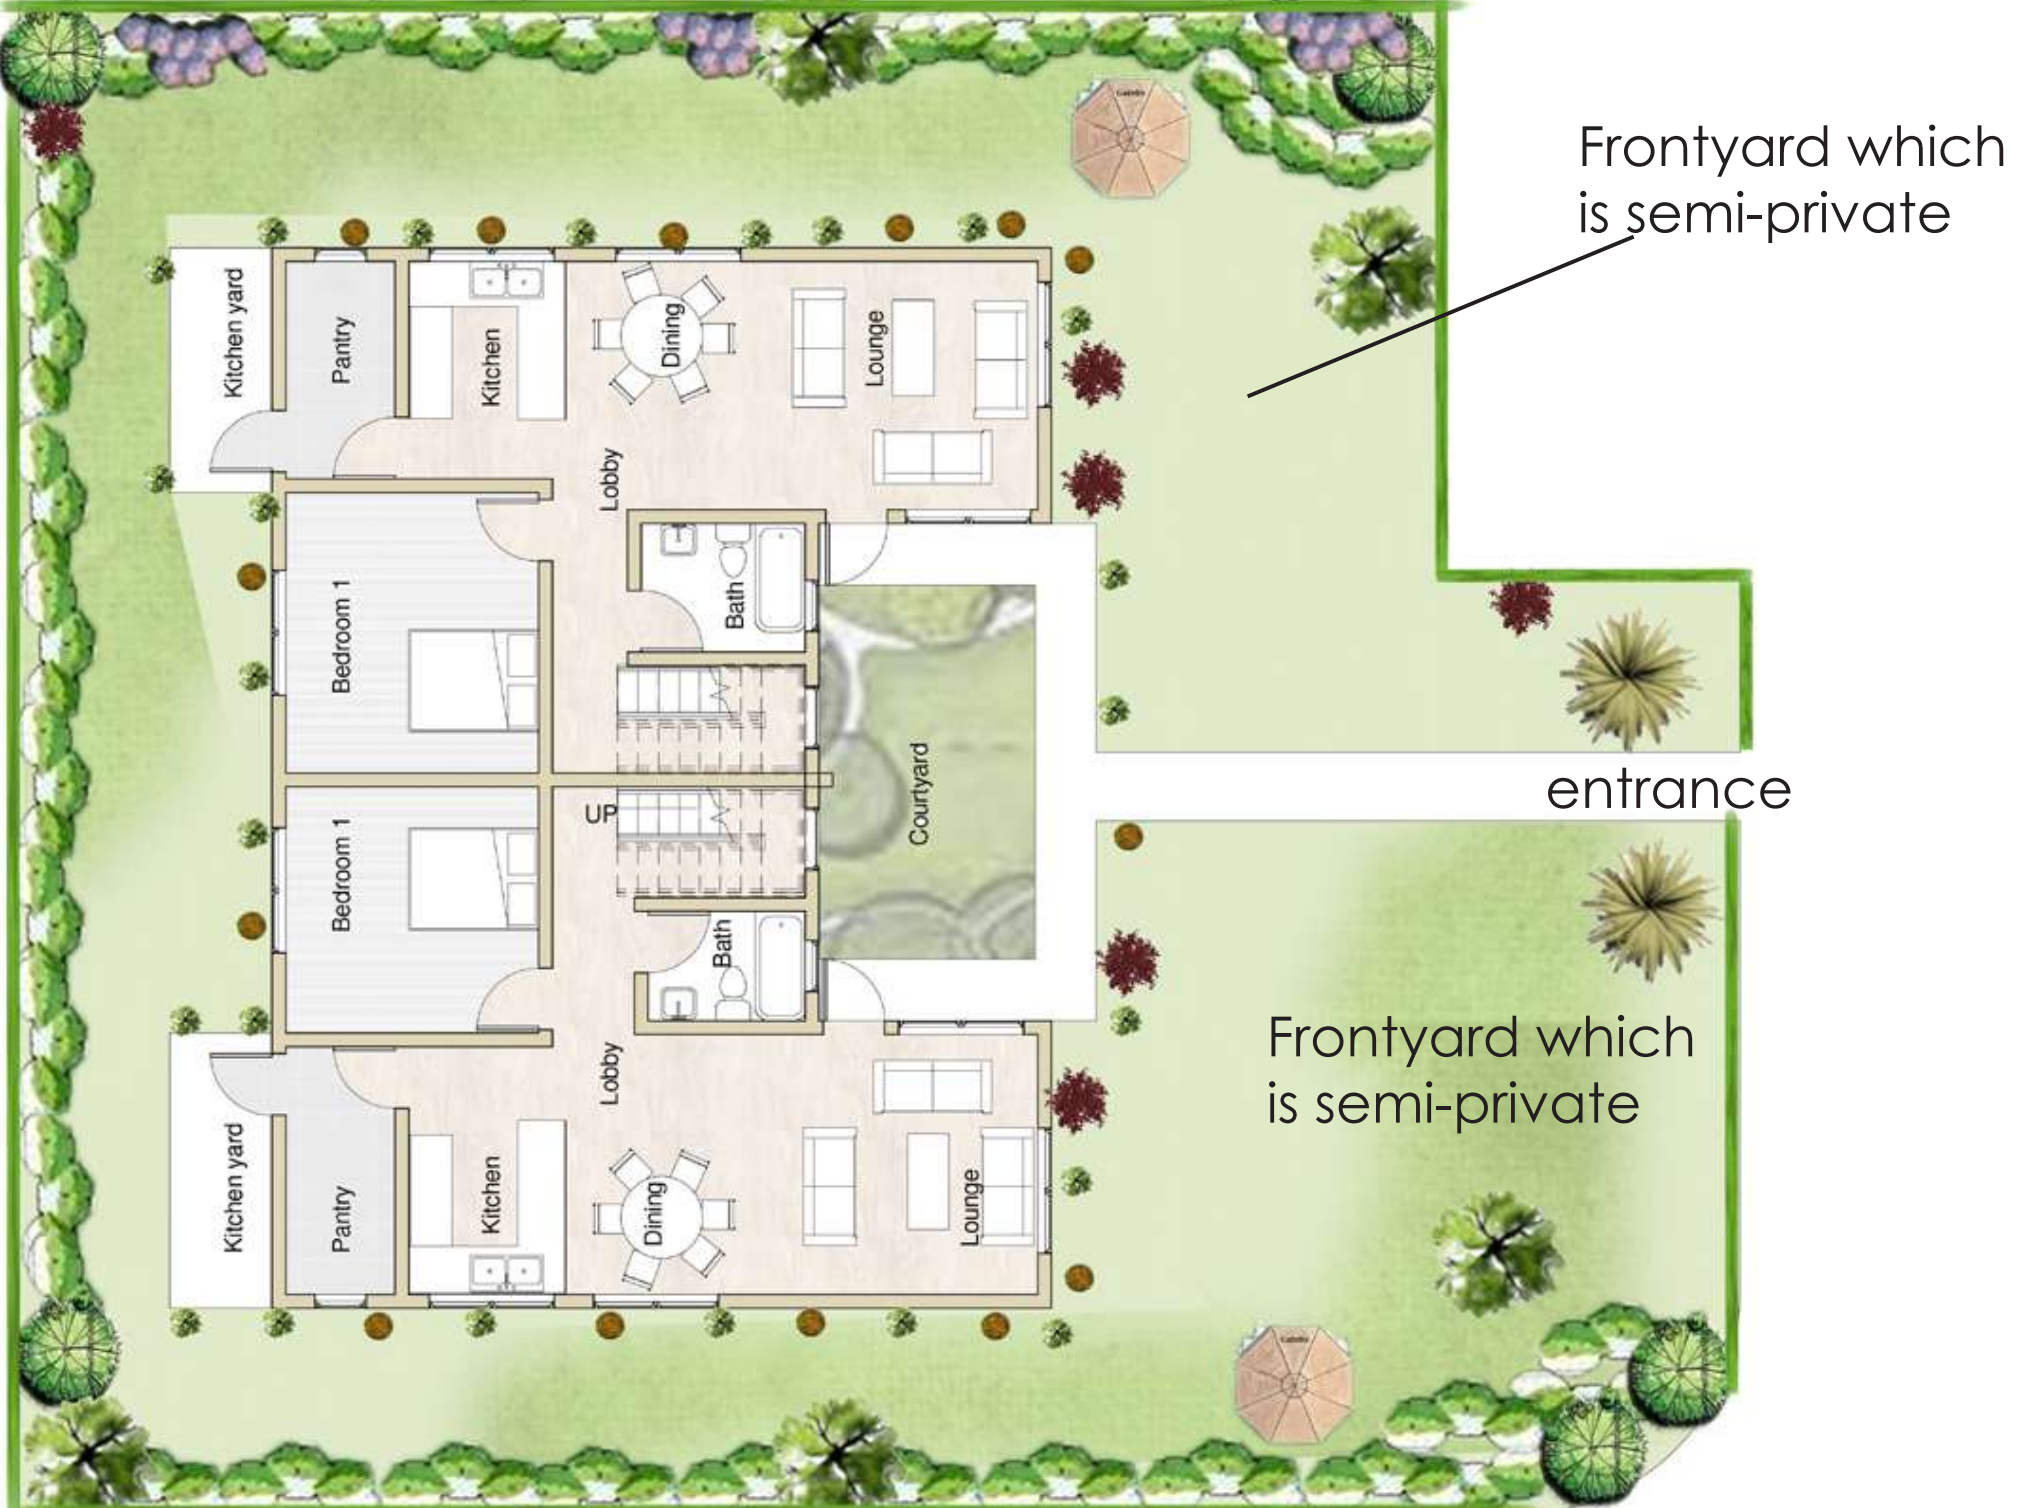


CONSTRUCTION IN PHASES- PHASE -01

The maisonette can be constructed into different stages of several rooms at a go



CLUSTER PLAN

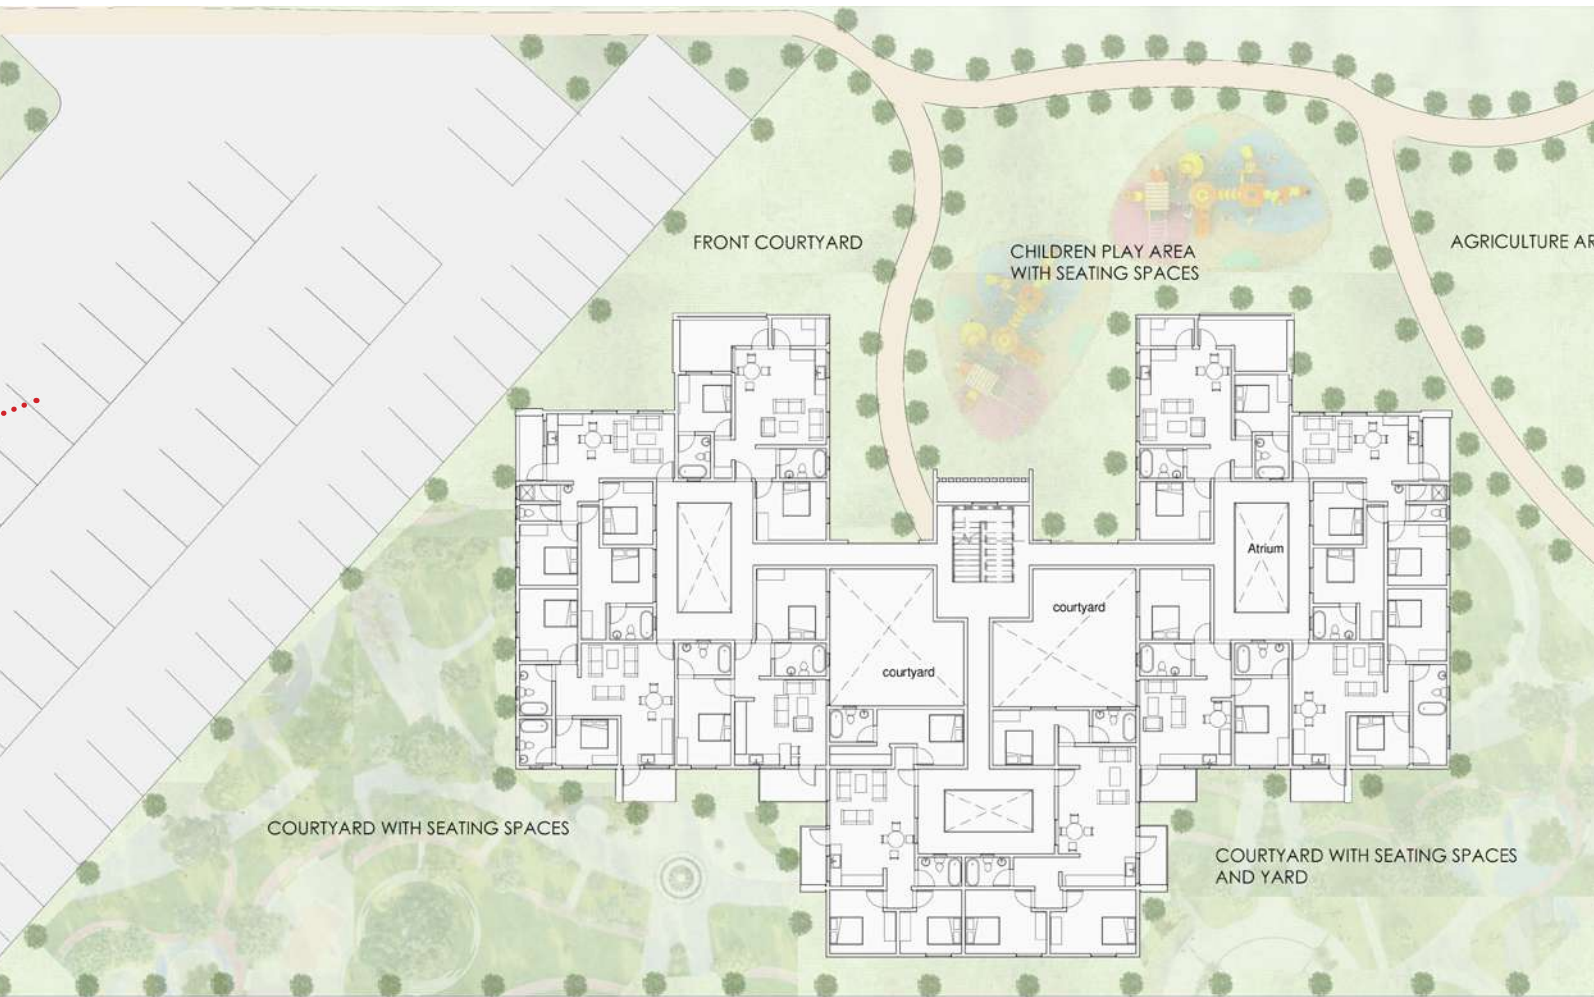

CLUSTER ELEVATION-01

CLUSTER 3D RENDER



CLUSTER ELEVATION-02

BACK ELEVATION



FRONT ELEVATION




3D VIEW




UNIT 3D RENDER




TYPICAL FLOOR PLAN

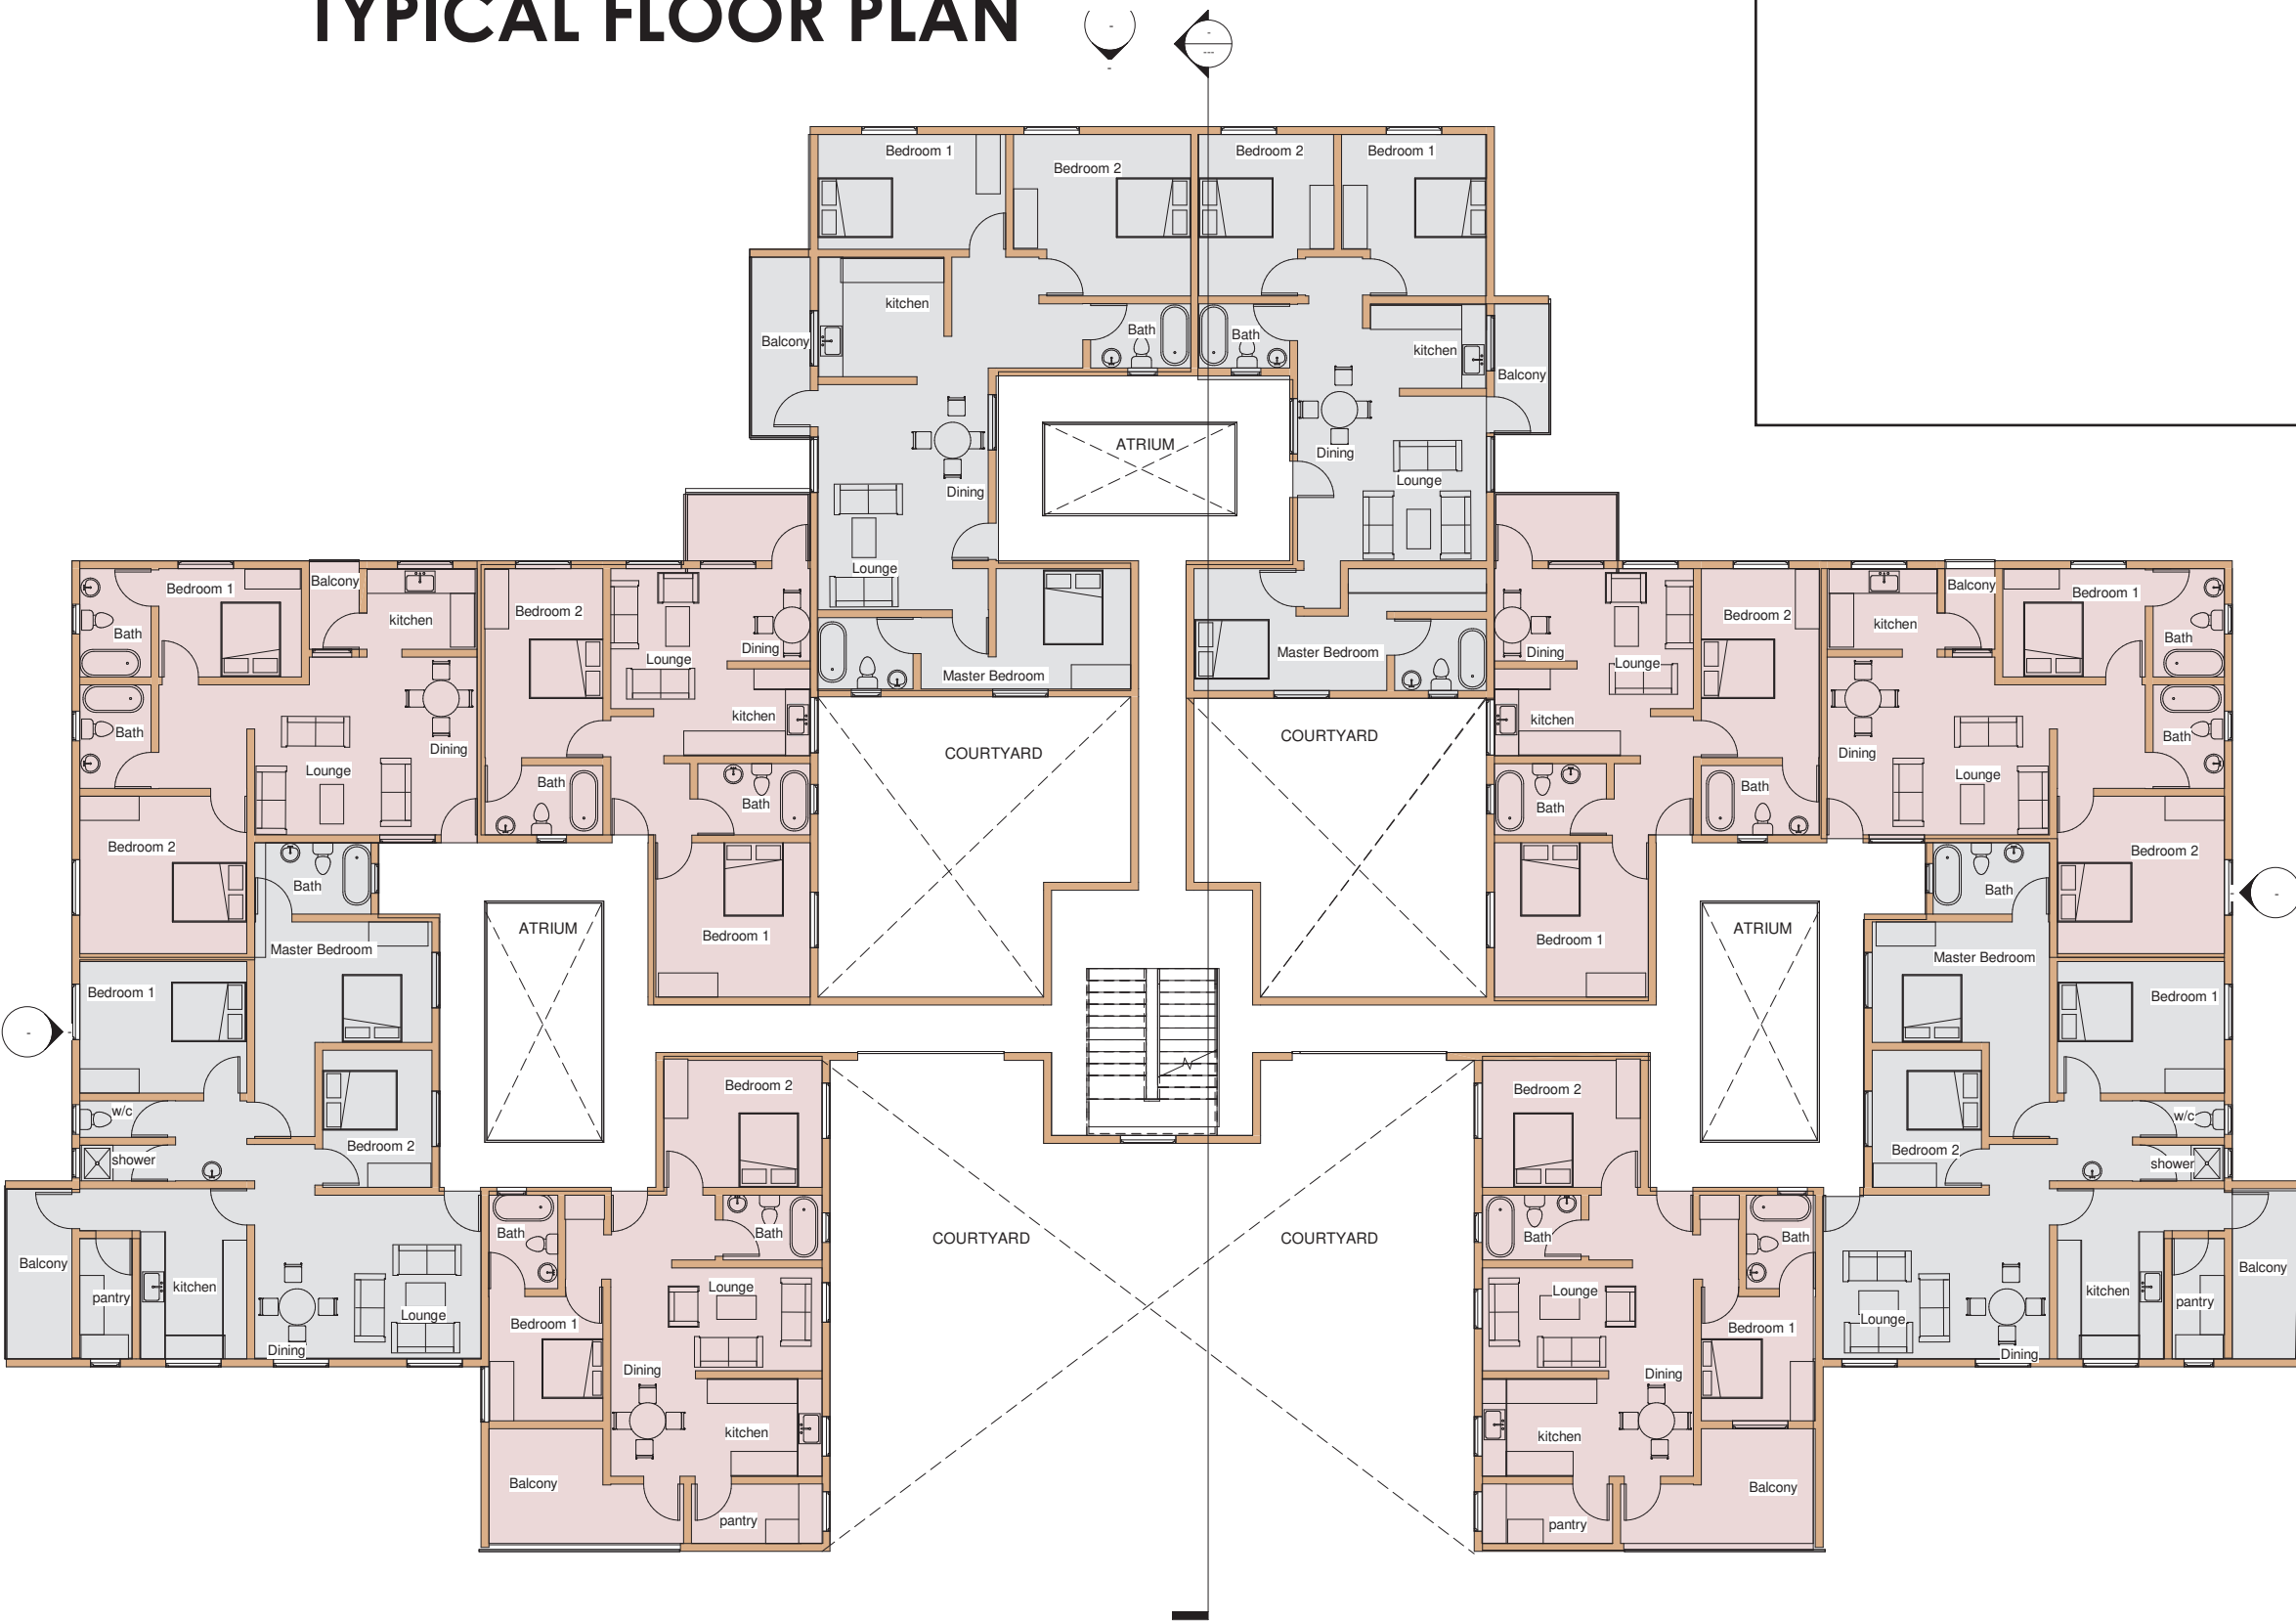


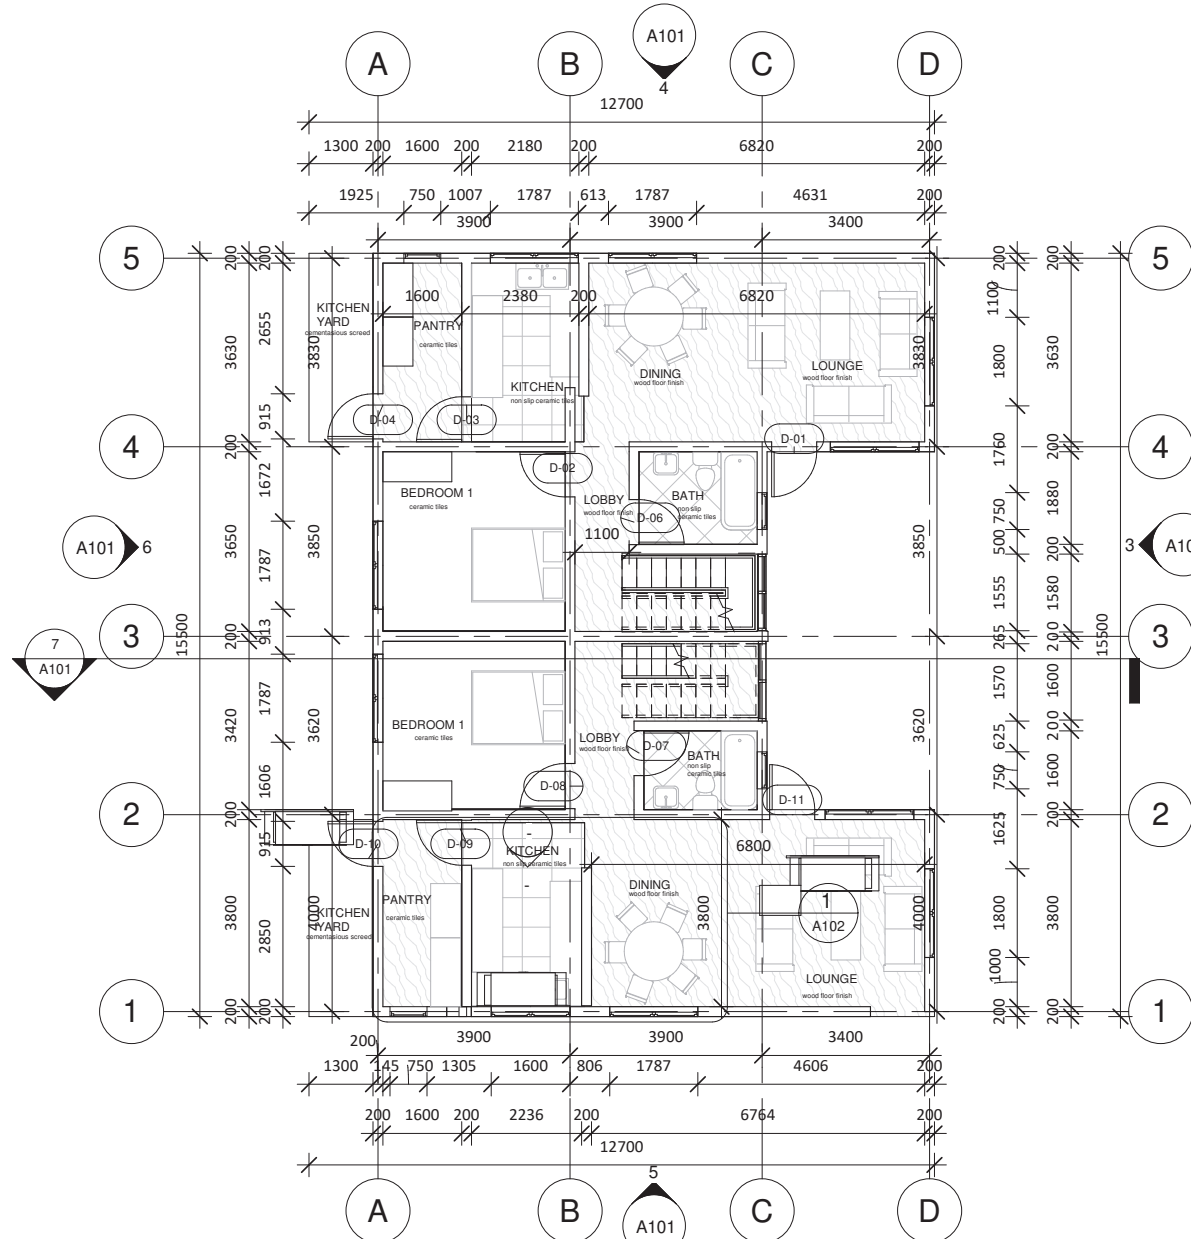


SEMI-DETACHED MAISONETTE FIRST FLOOR
SCALE 1:100

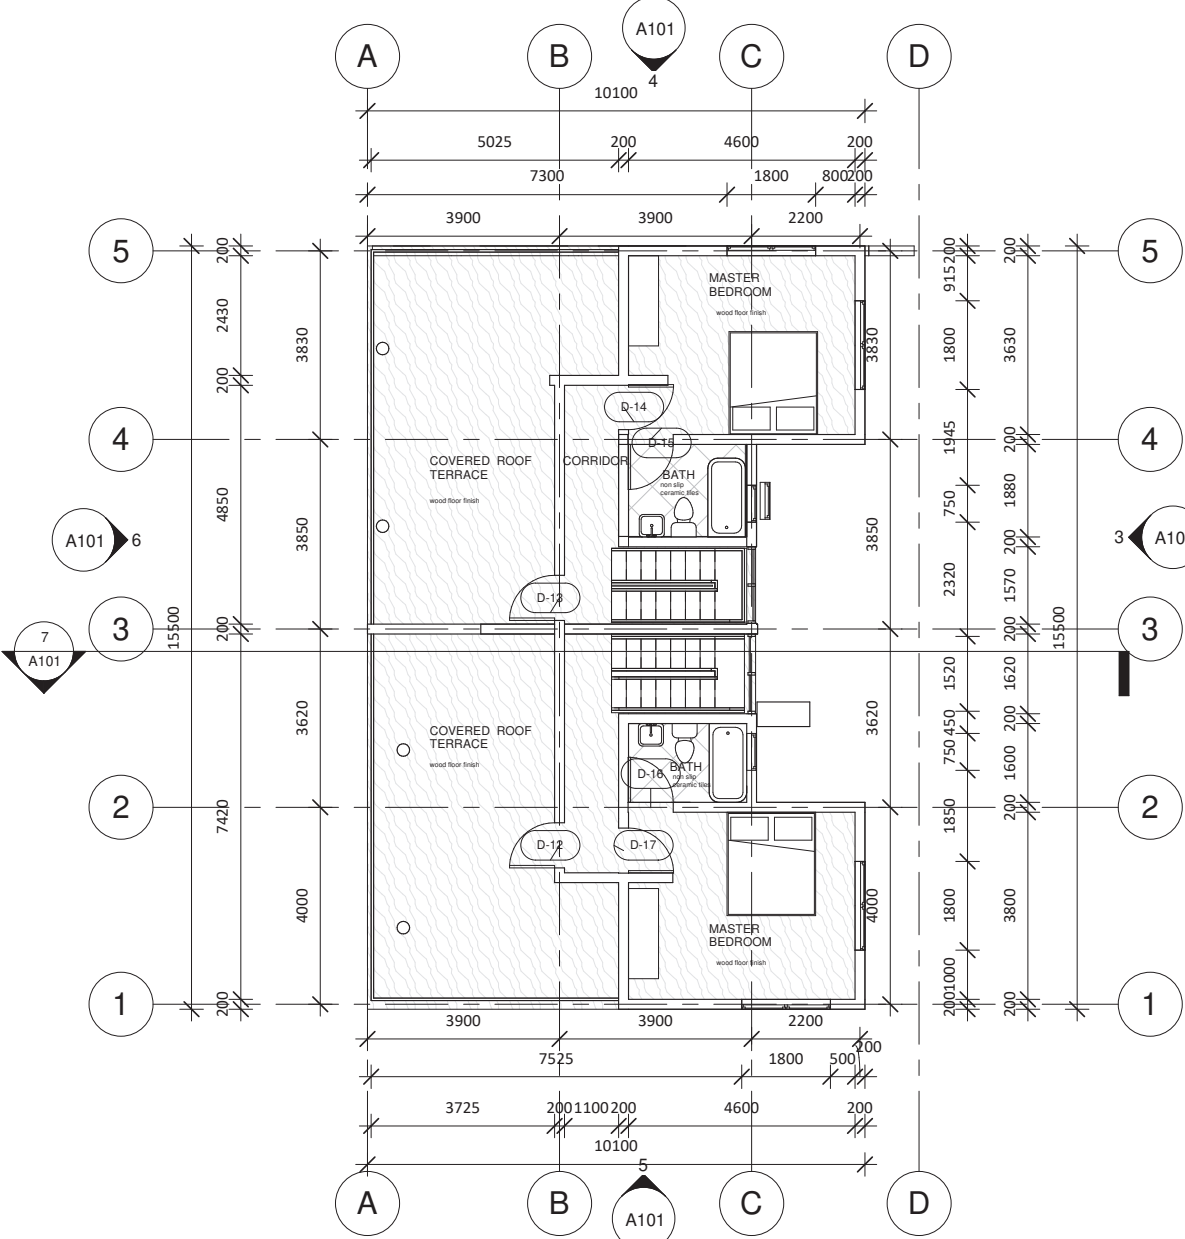


SEMI-DETACHED MAISONETTE GROUND FLOOR
SCALE 1:100

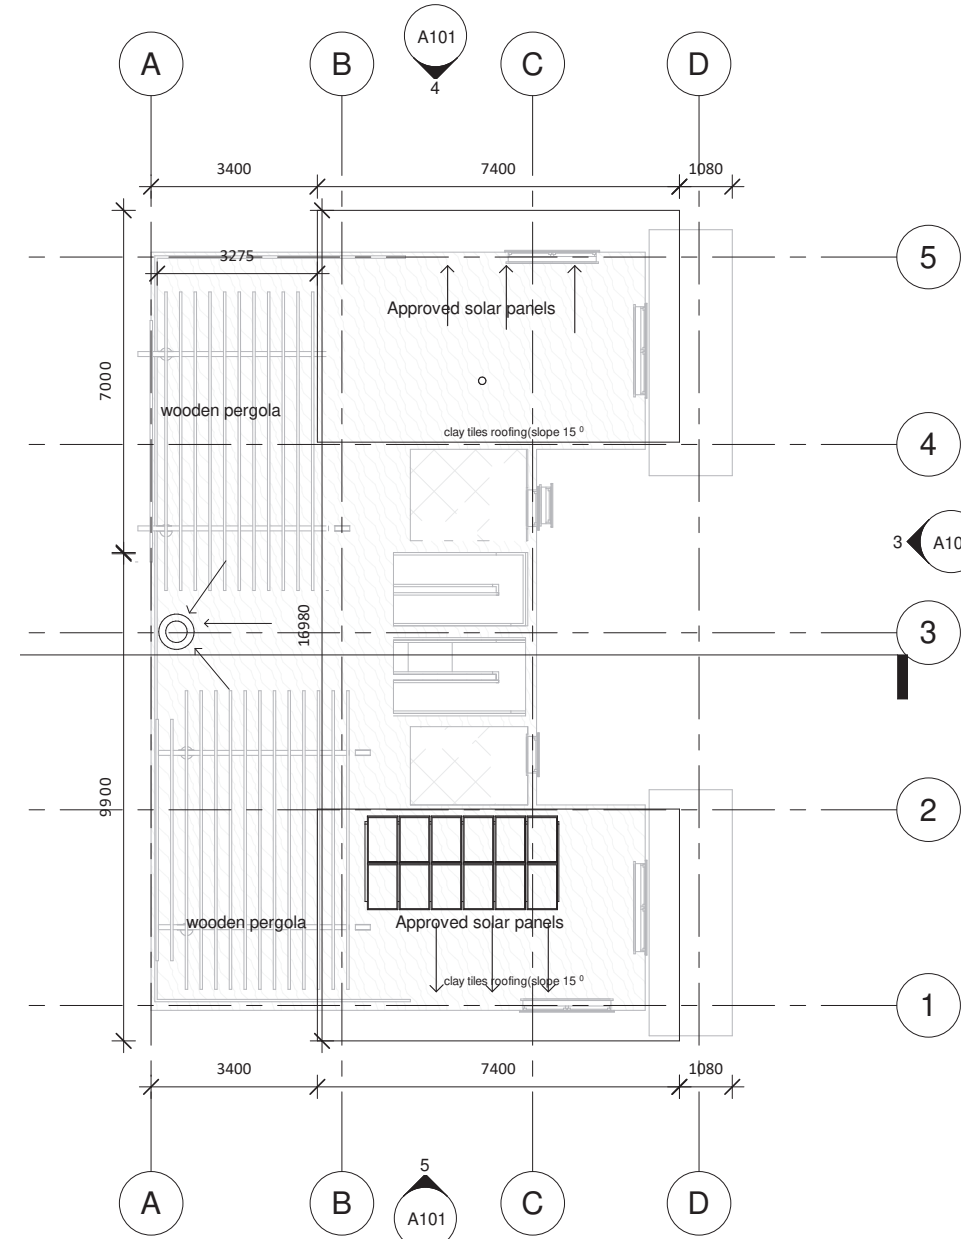


SEMI-DETACHED MAISONETTE ROOF PLAN
SCALE 1:100

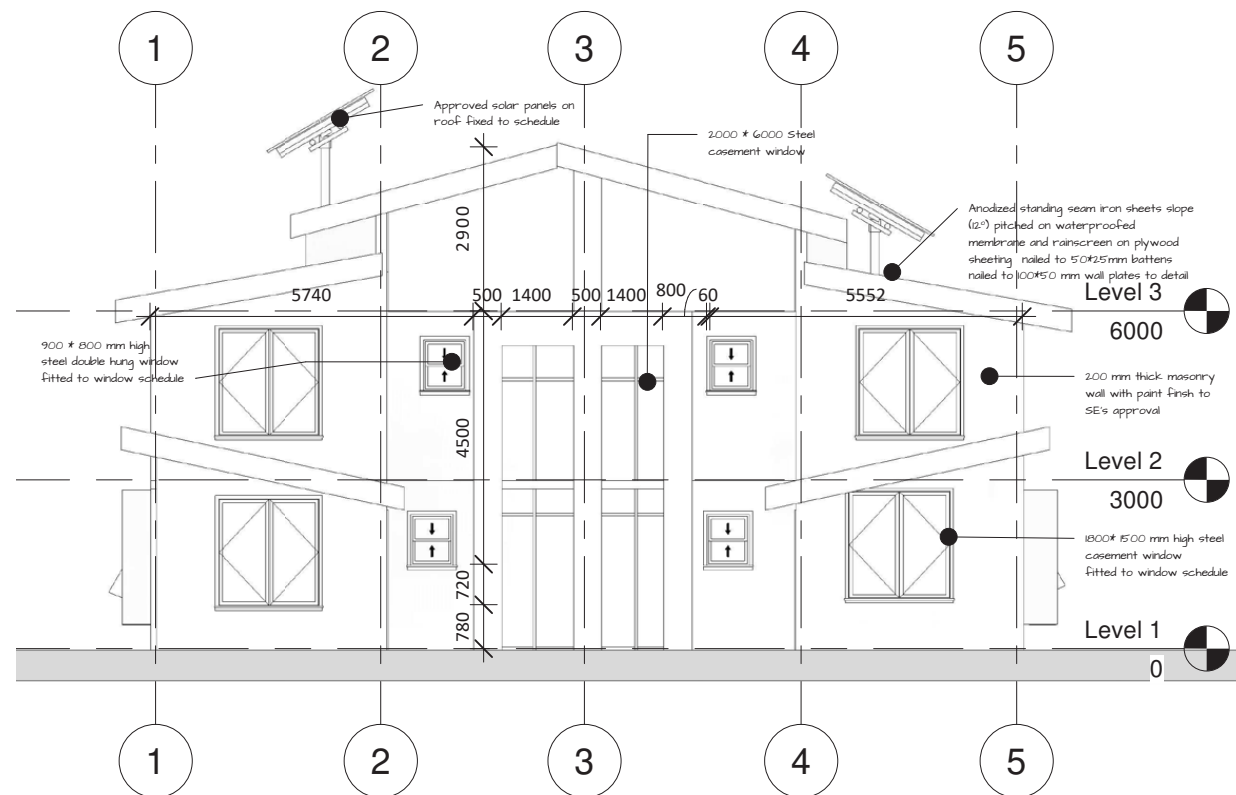


SEMI-DETACHED MAISONETTE FRONT ELEVATION
SCALE 1:100

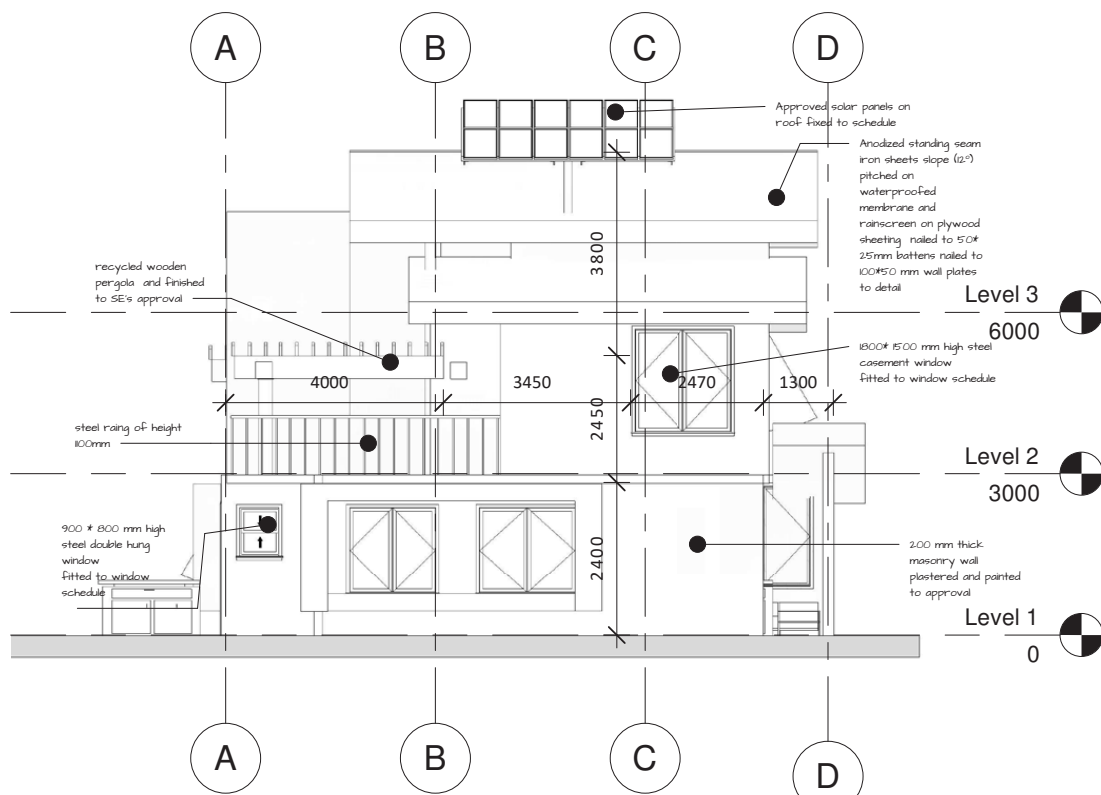


SEMI-DETACHED MAISONETTE SIDE ELEVATION
SCALE 1:100

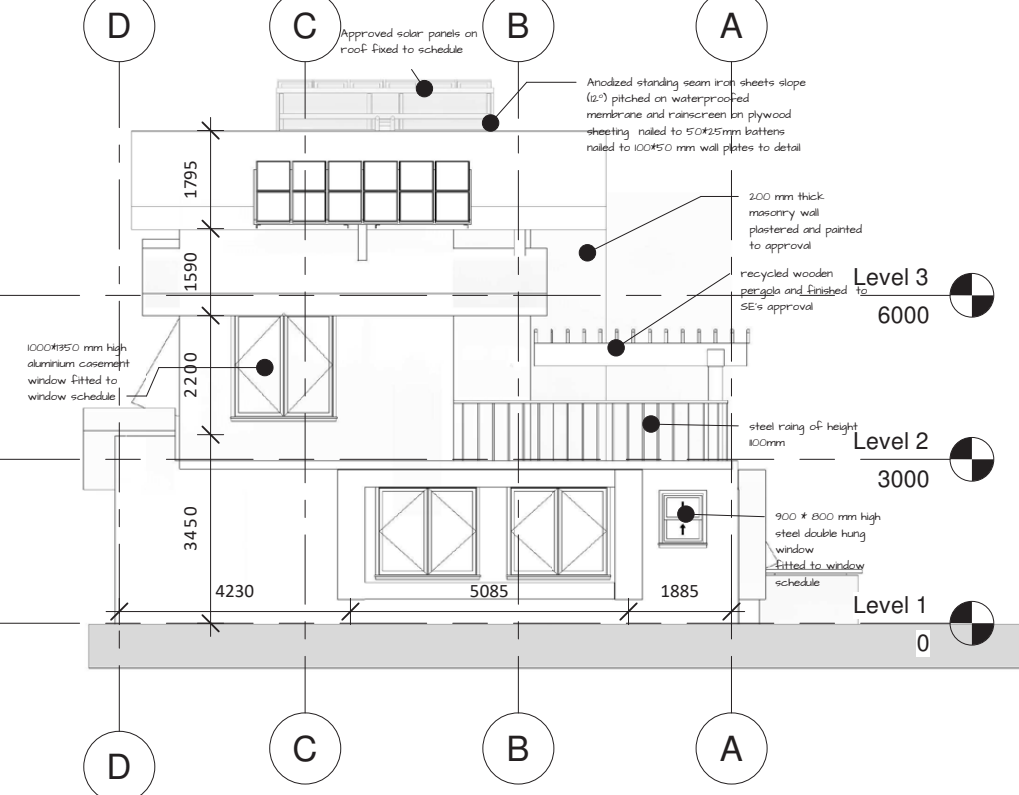


ROOF DETAIL

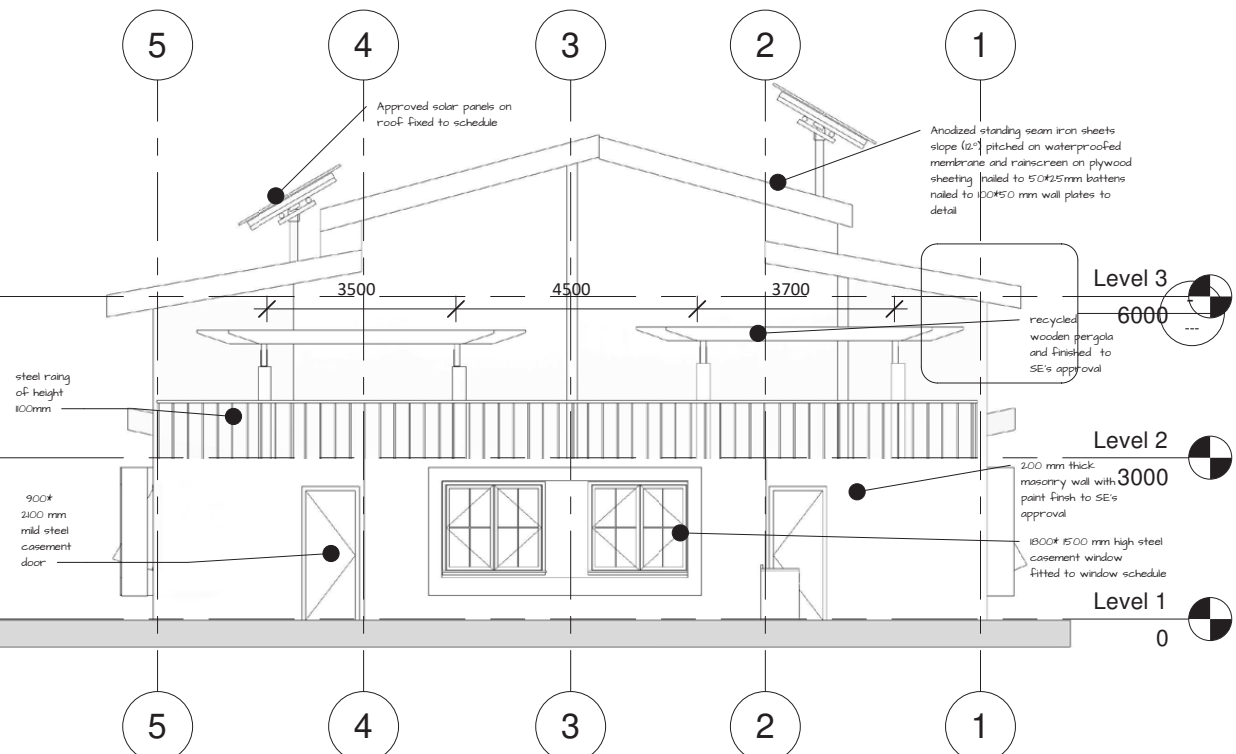

SEMI-DETACHED MAISONETTE BACK ELEVATION
SCALE 1:100

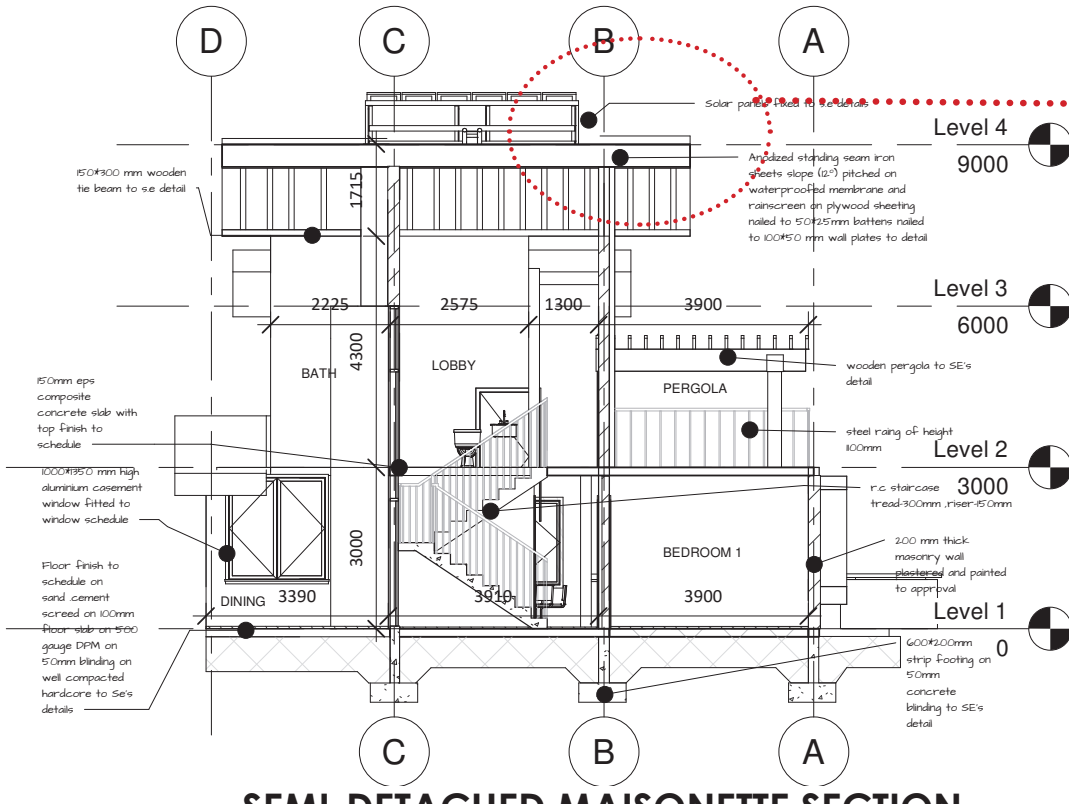

SEMI-DETACHED MAISONETTE SECTION
SCALE 1:100

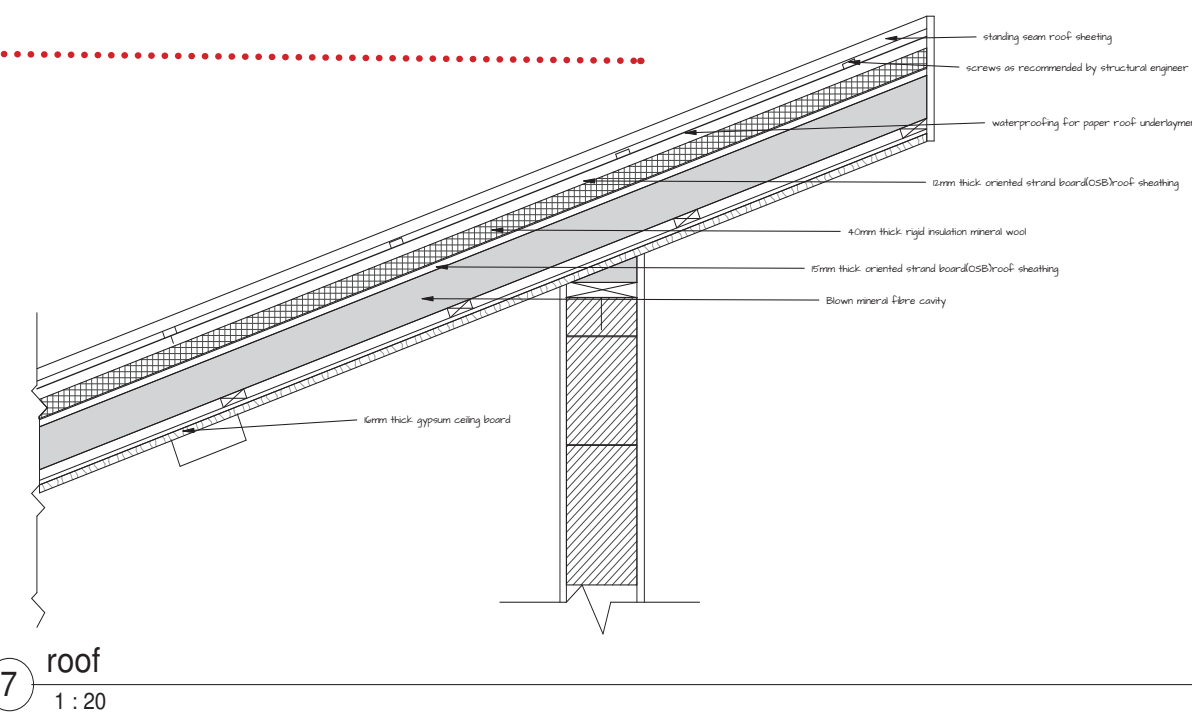

7 roof
1:20

03 URBAN HOUSING CLUSTER DESIGN

BRIEF: A housing society consisting of 80- 100 units that includes:

3 bedroom bungalow

4 bedroom bungalow

3 bedroom maisonette

4 bedroom maisonette

2& 3 bedroom apartment

which includes the following aspects; SPACE
SHARING, FORMALITY & TRANSFORMATION
community centre





ELEVATIONS:



PLAN:



APARTMENT
VIEW




04 : ECO-LODGE DESIGN


BRIEF: Design for ecology, sustainability,
adaptive re-use, Green Design, Organic
design 20 bed ecolodge







FLOOR PLAN

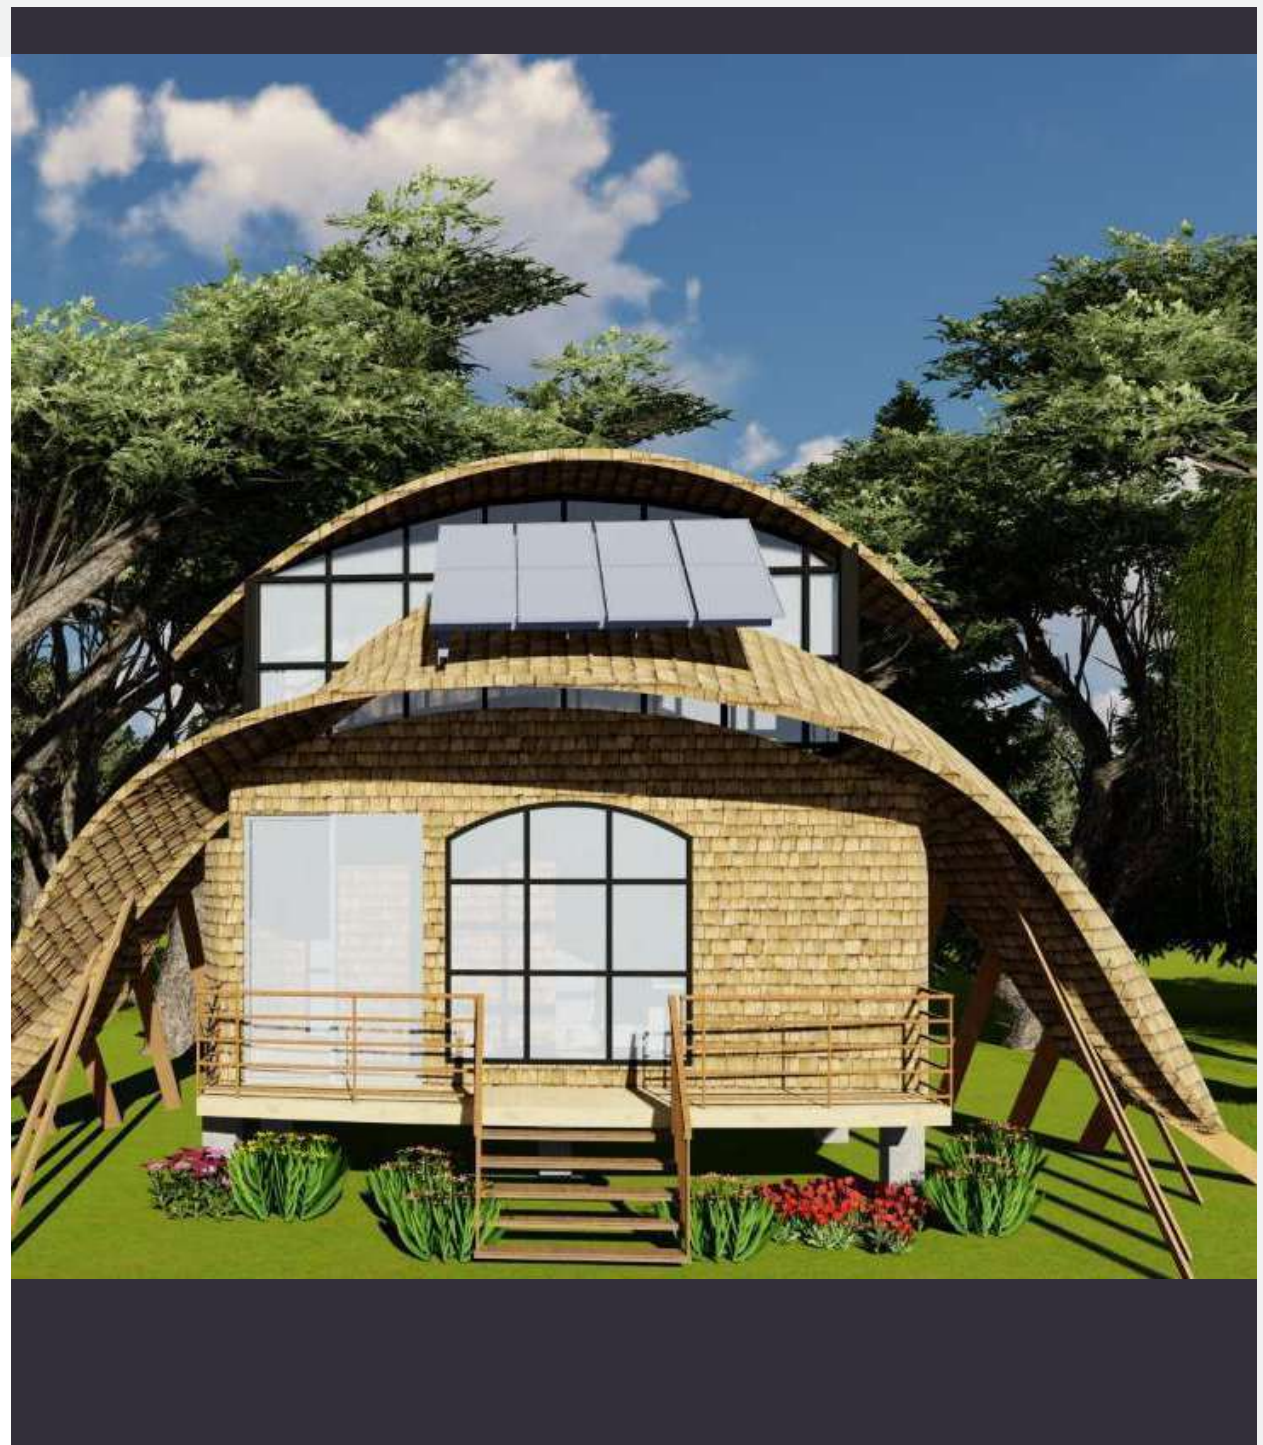


ELEVATIONS

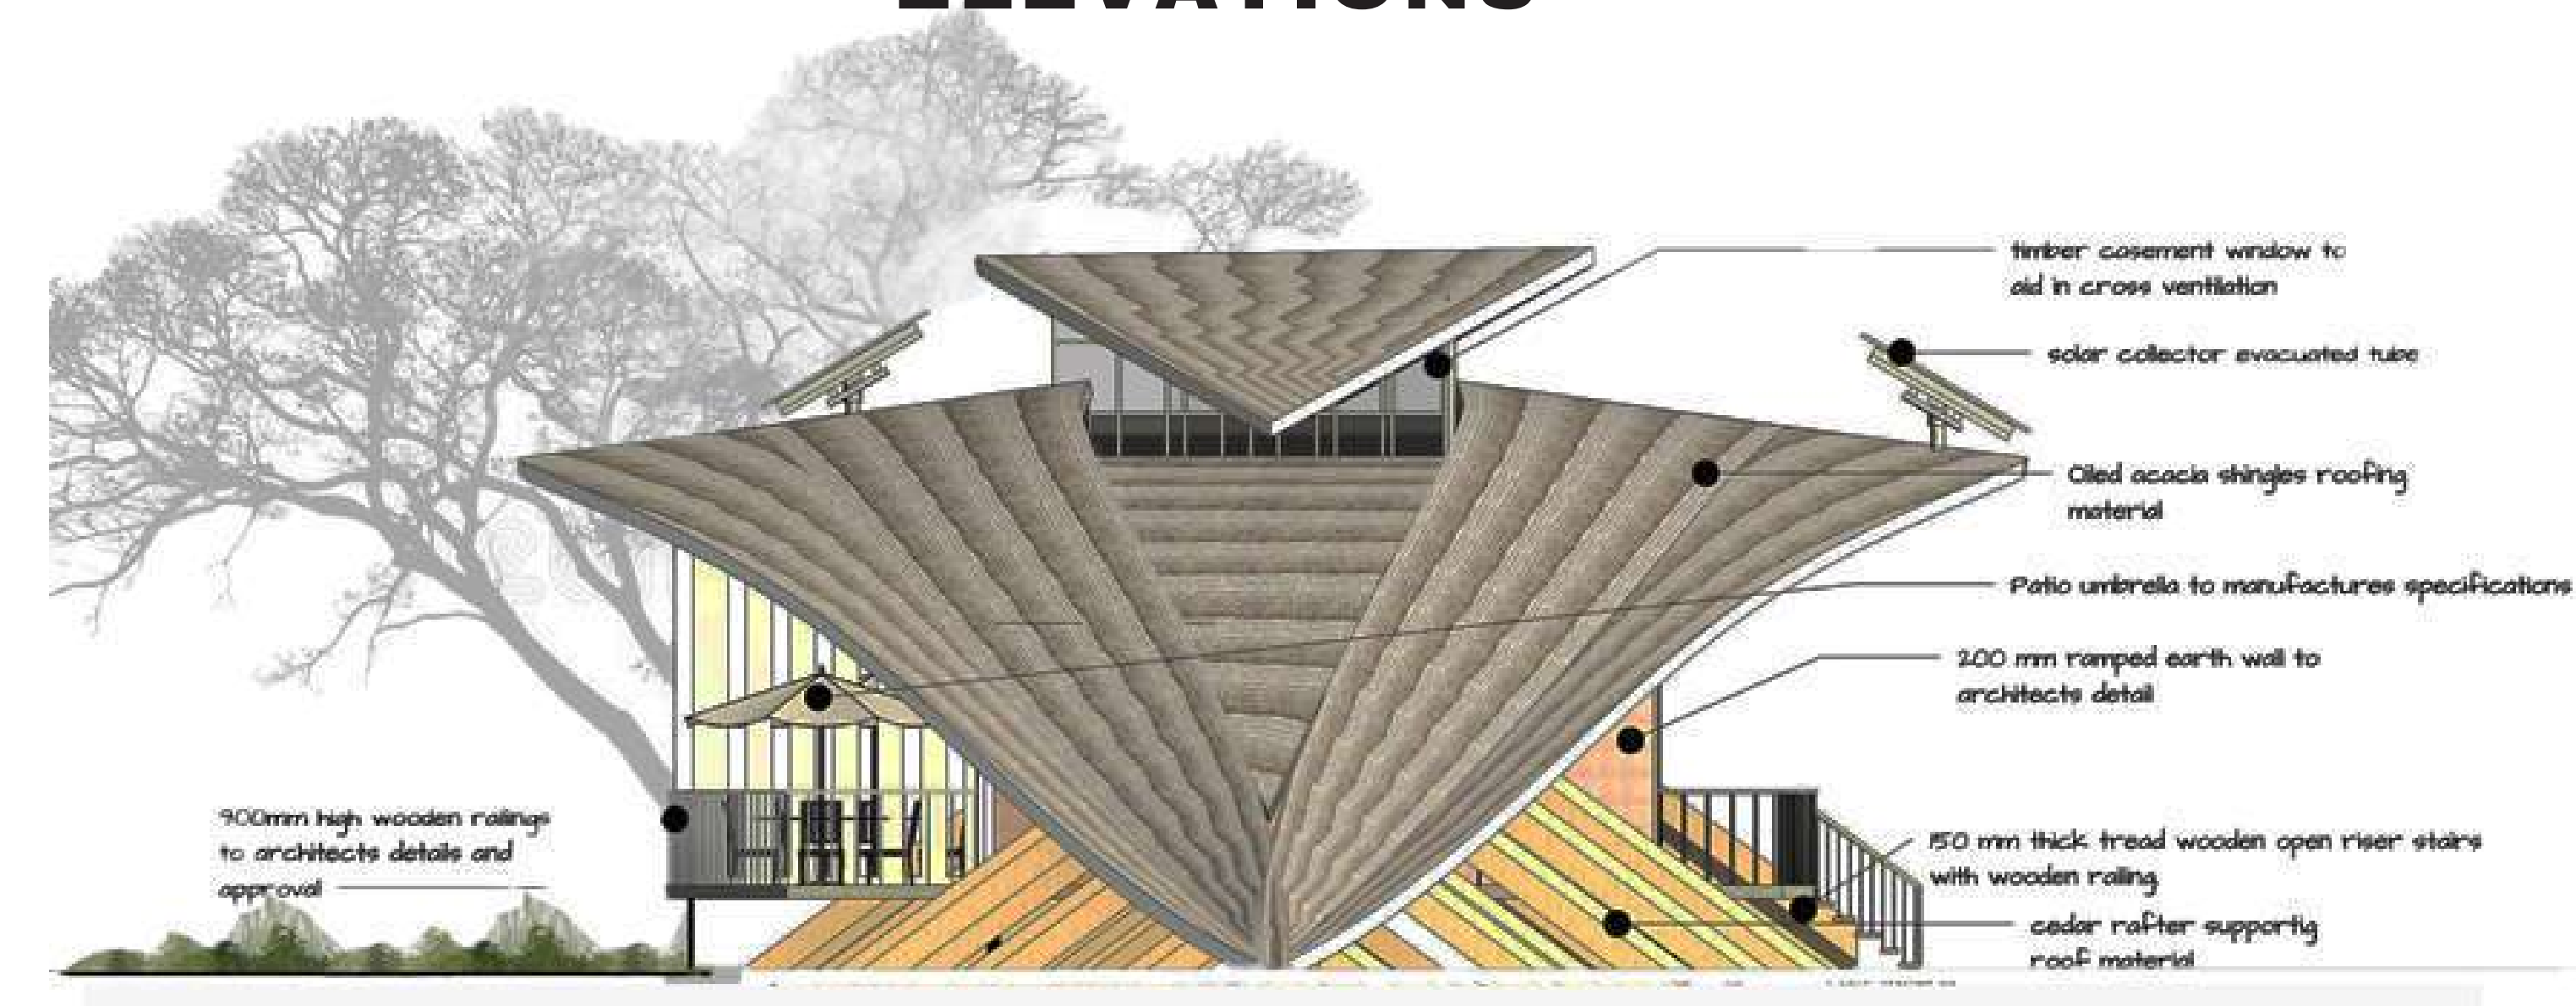

SPA & SAUNA

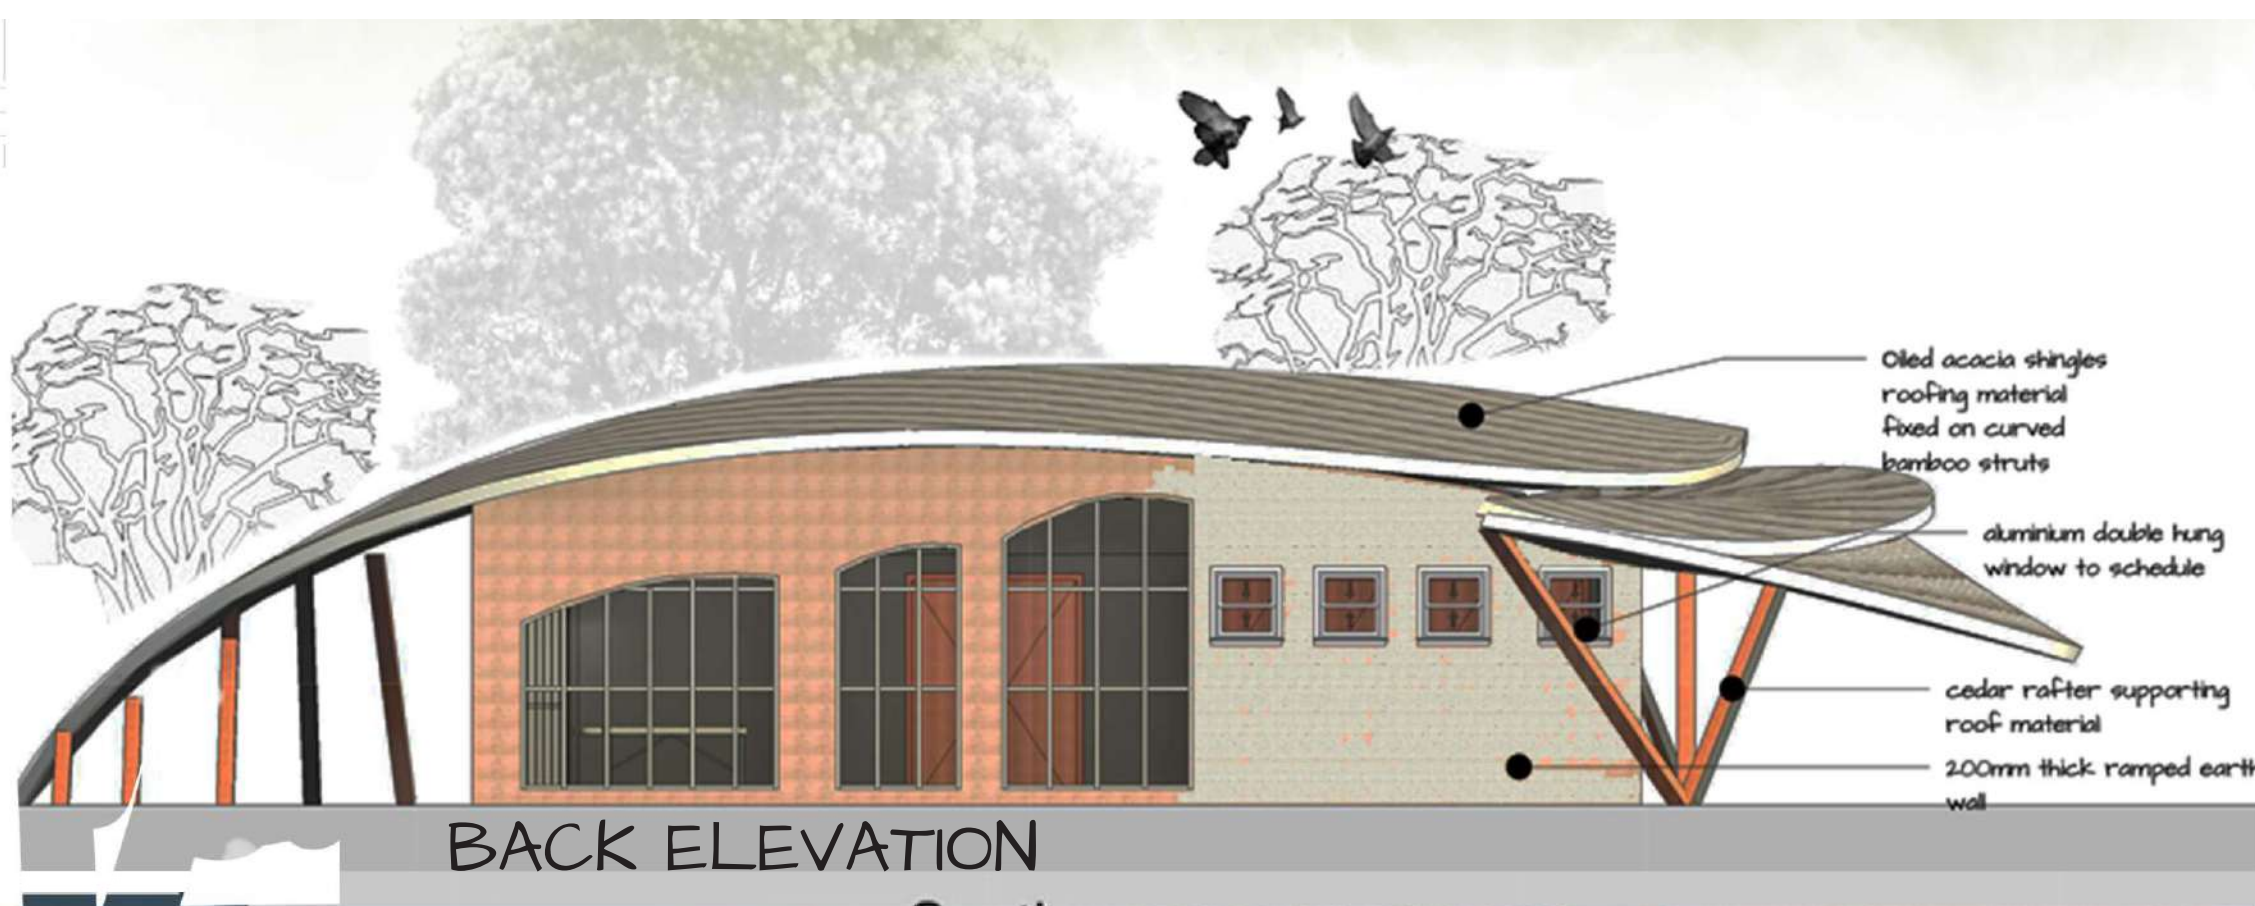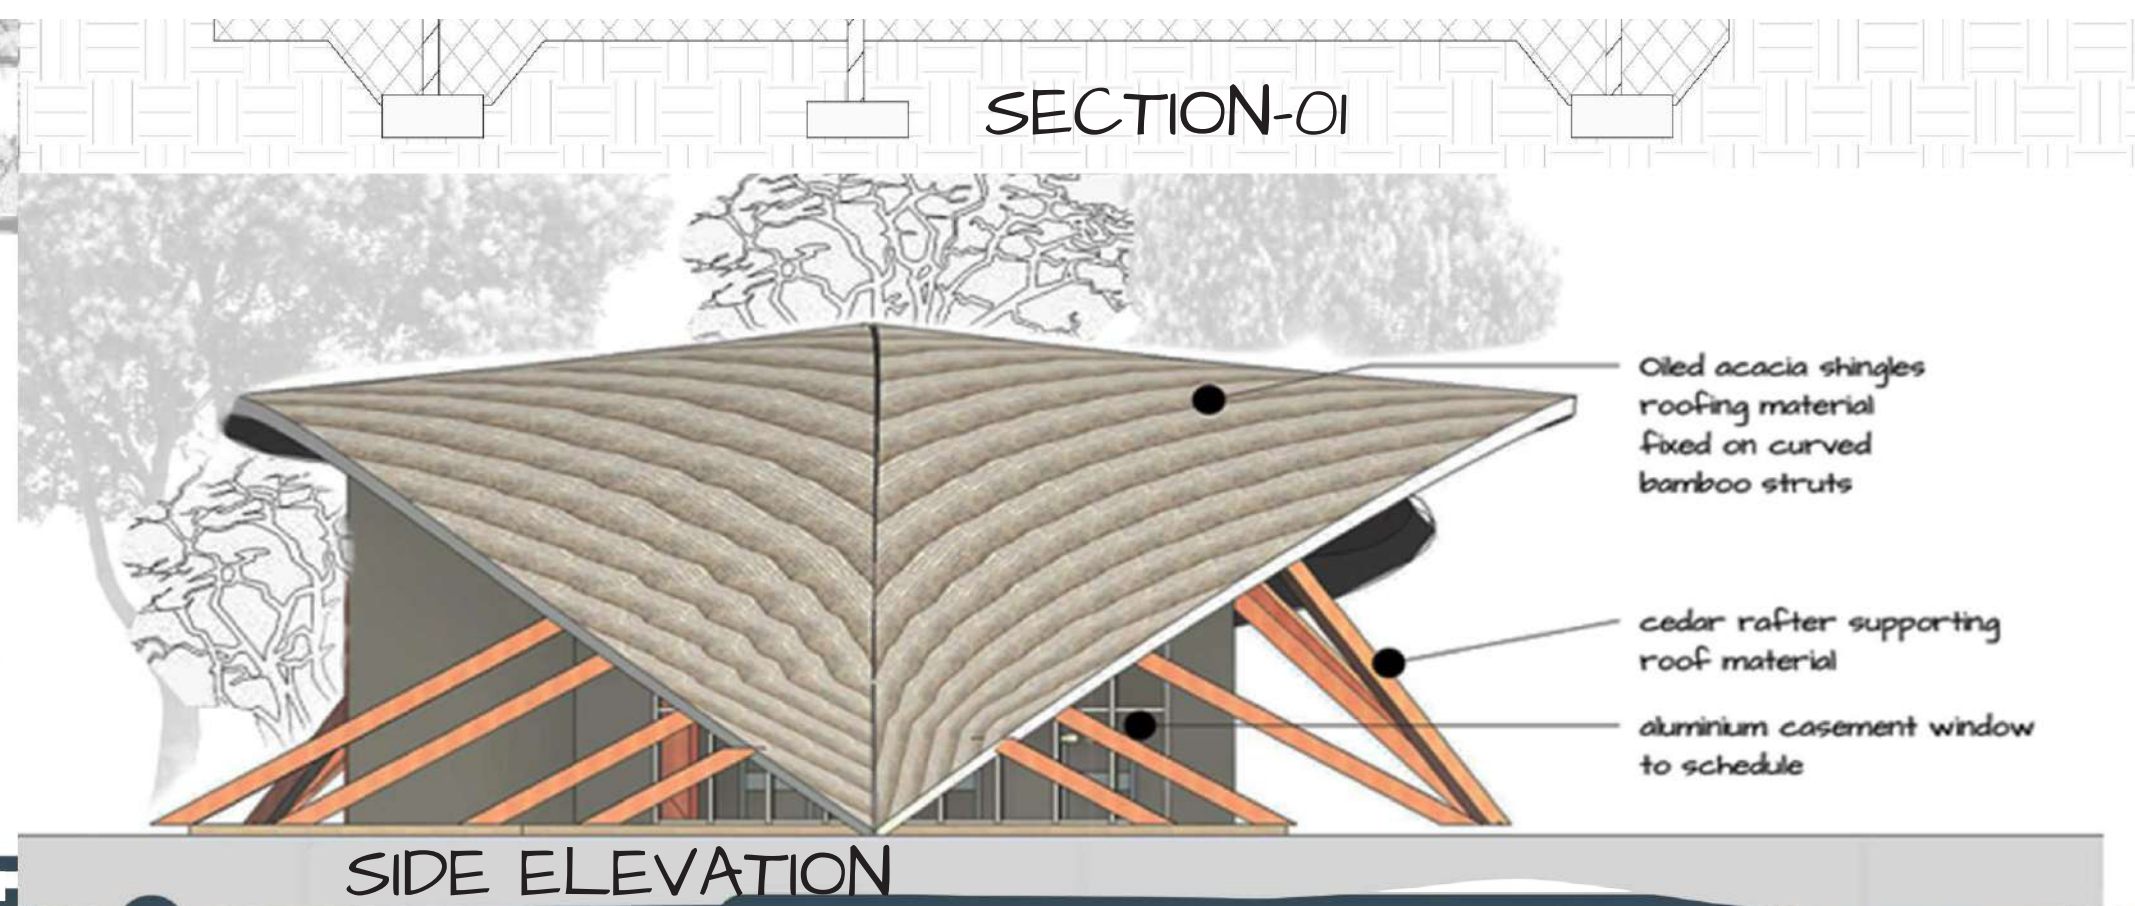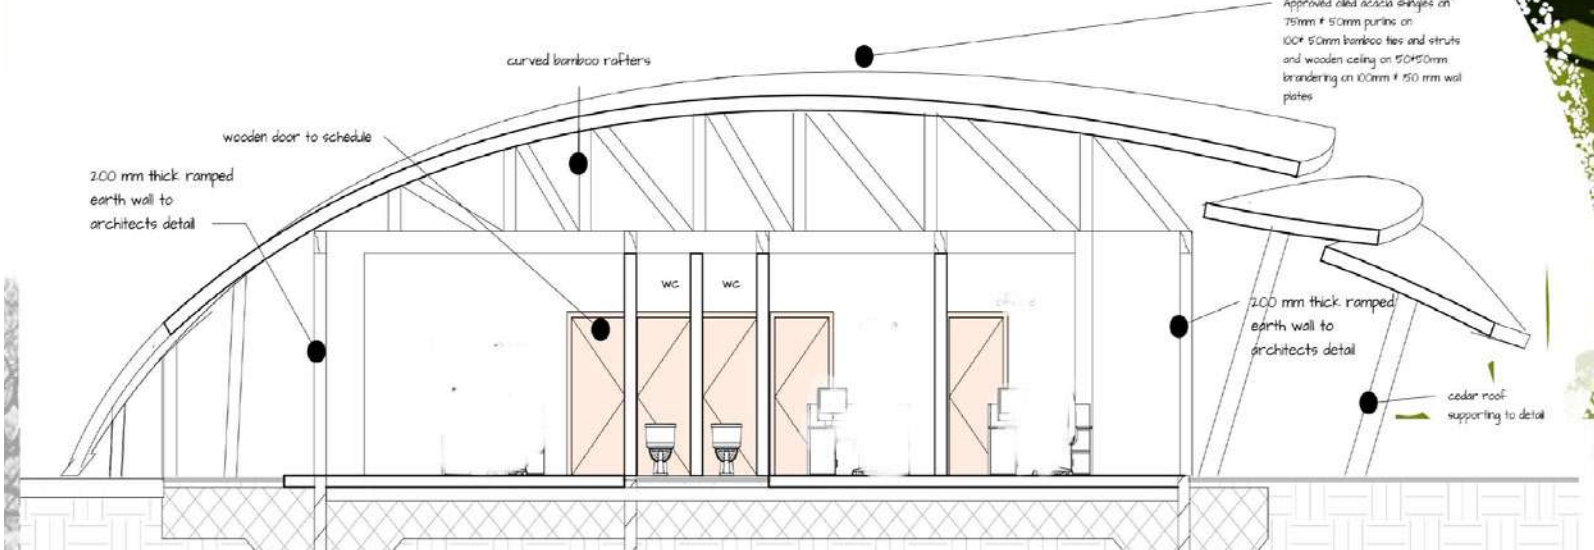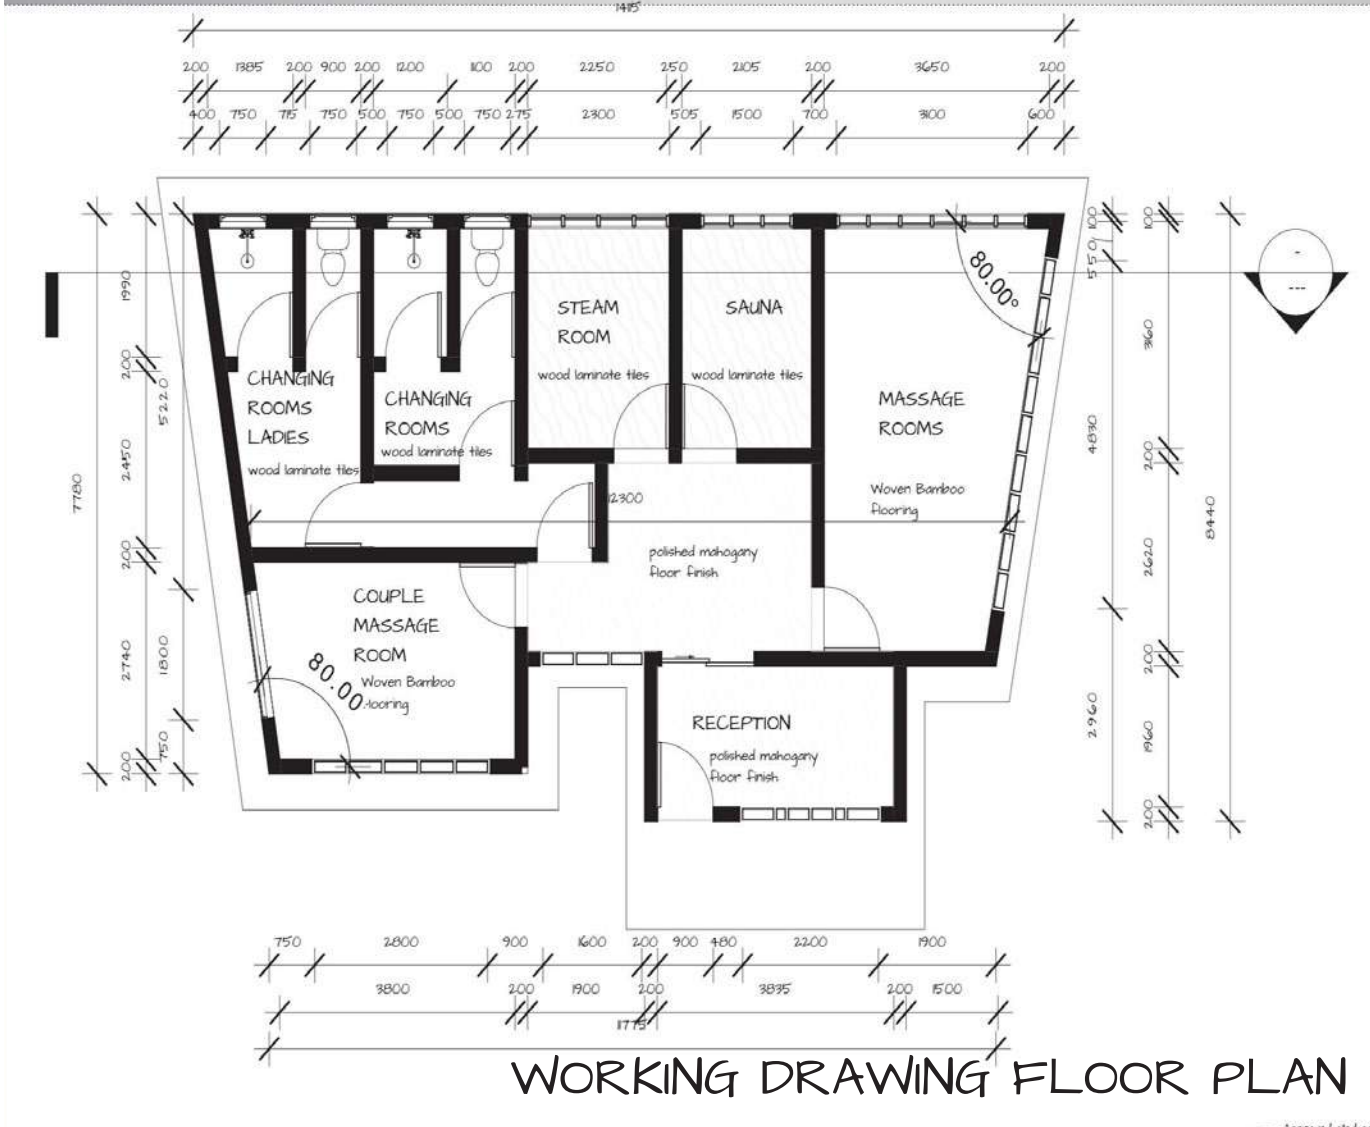


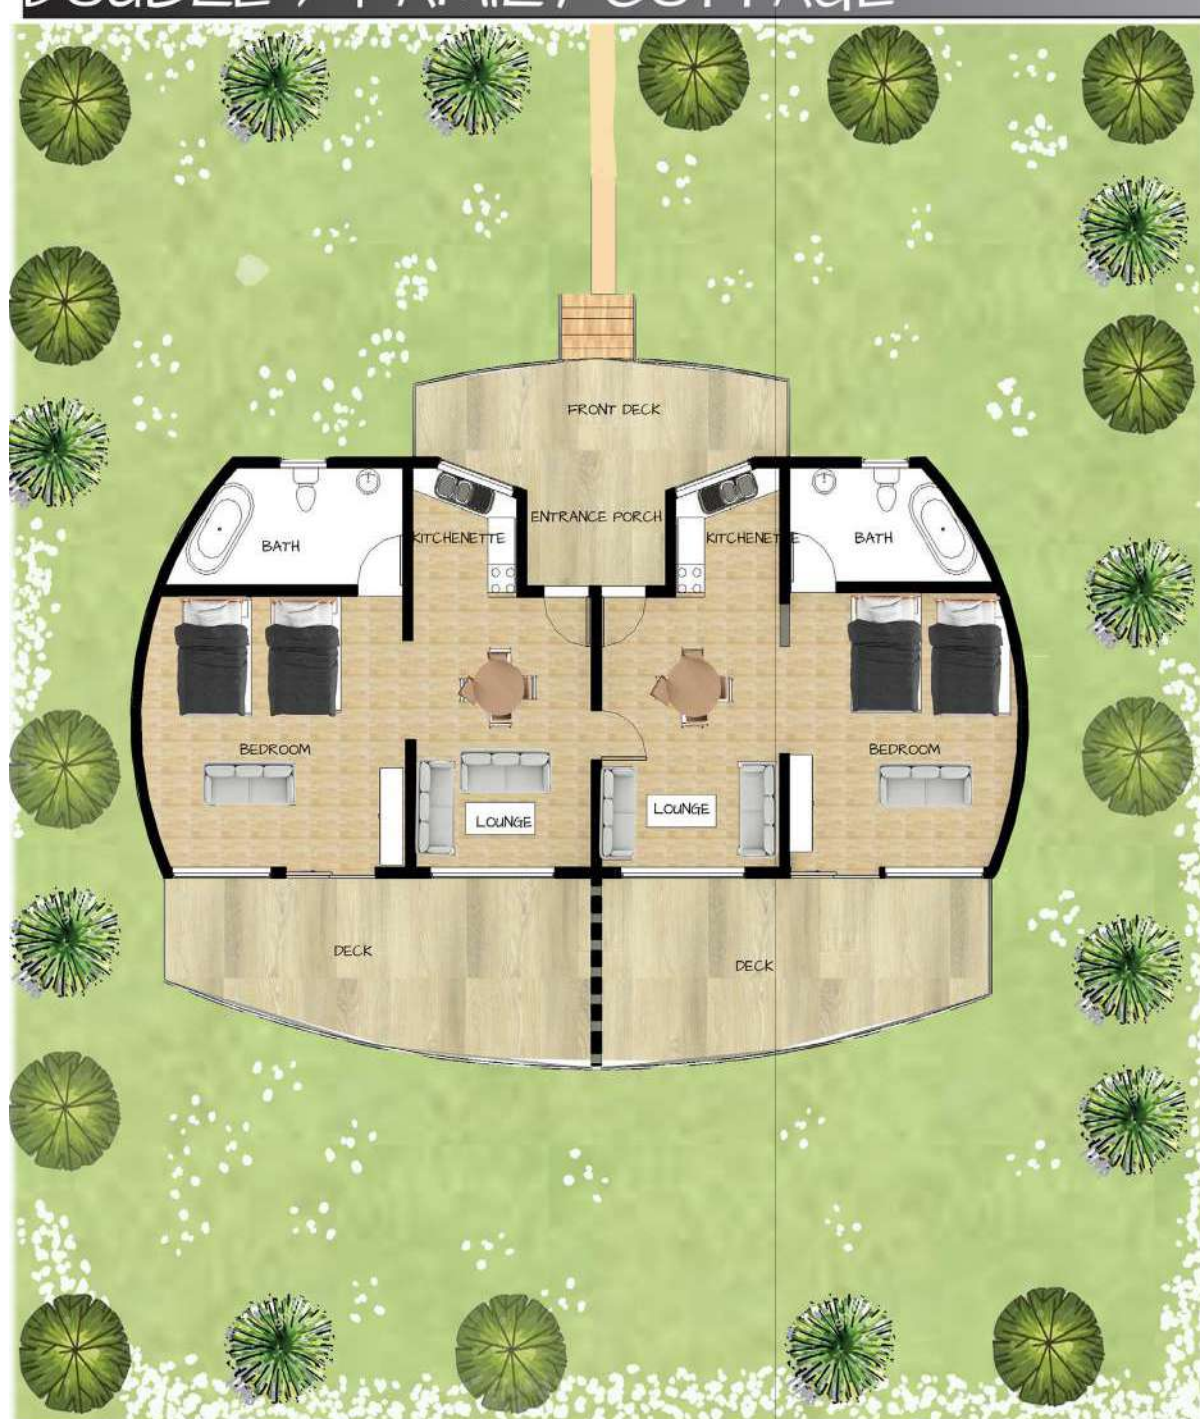


FLOOR PLAN




3D VIEW

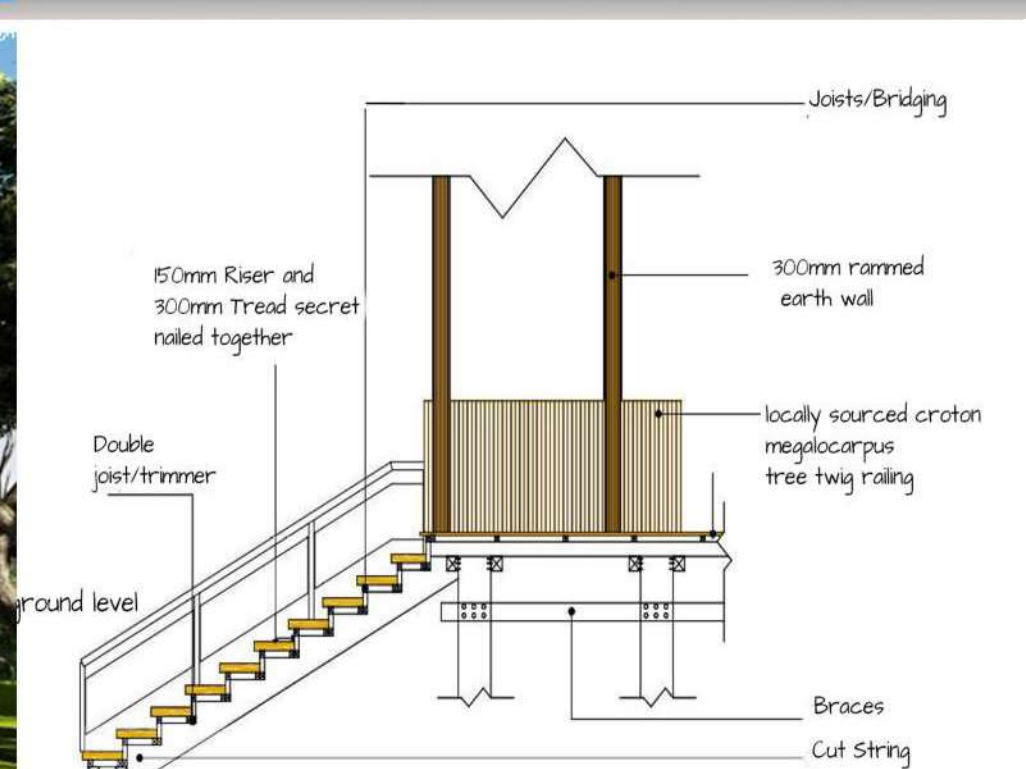


D-01 -OPEN RISER TIMBER STAIRS DETAIL

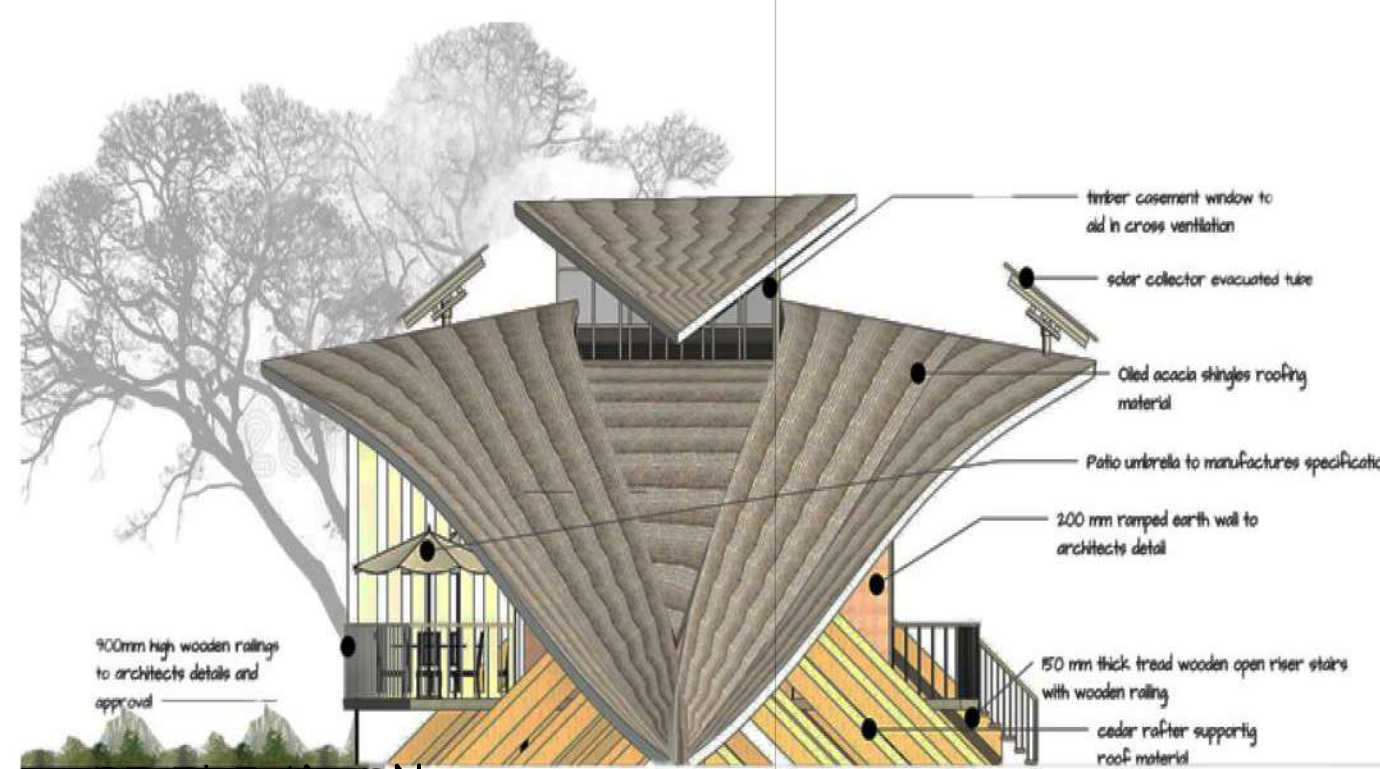


SIDE ELEVATION

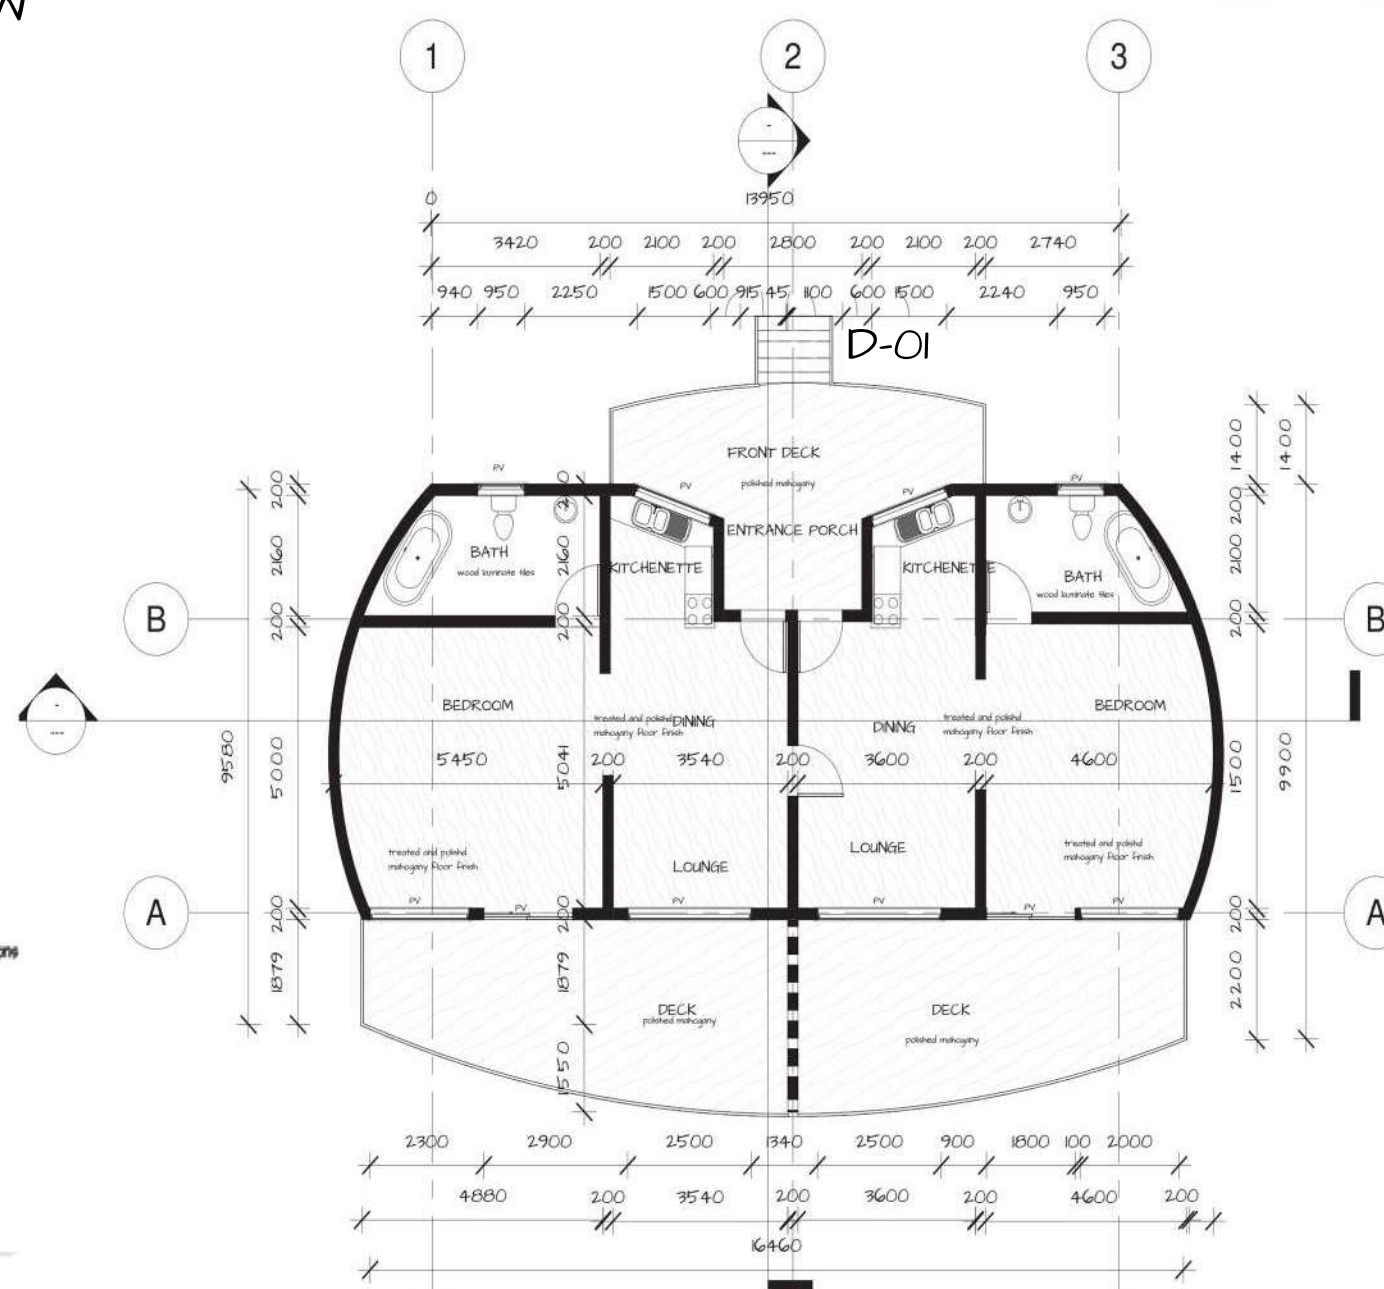


WORKING DRAWING²FLOOR PLAN³

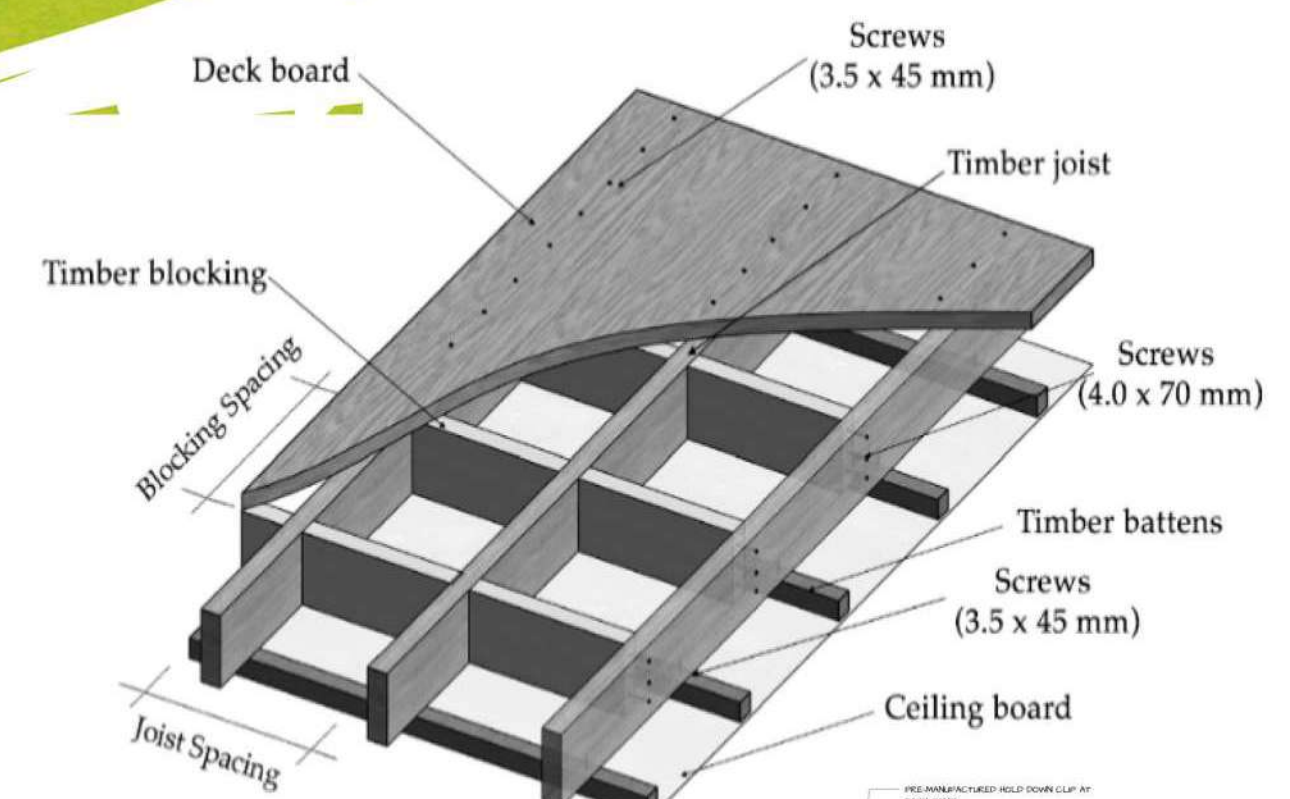

WOODEN FLOOR CONNECTION DETAIL

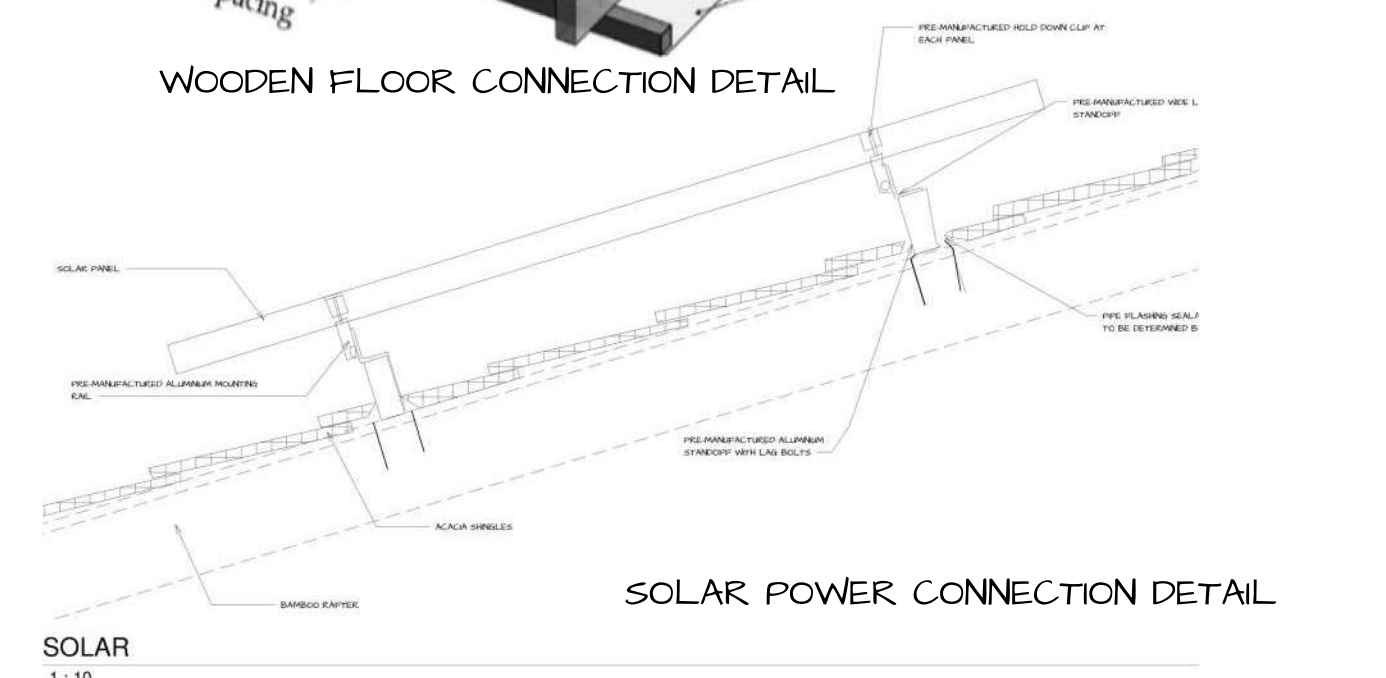


SOLAR POWER CONNECTION DETAIL

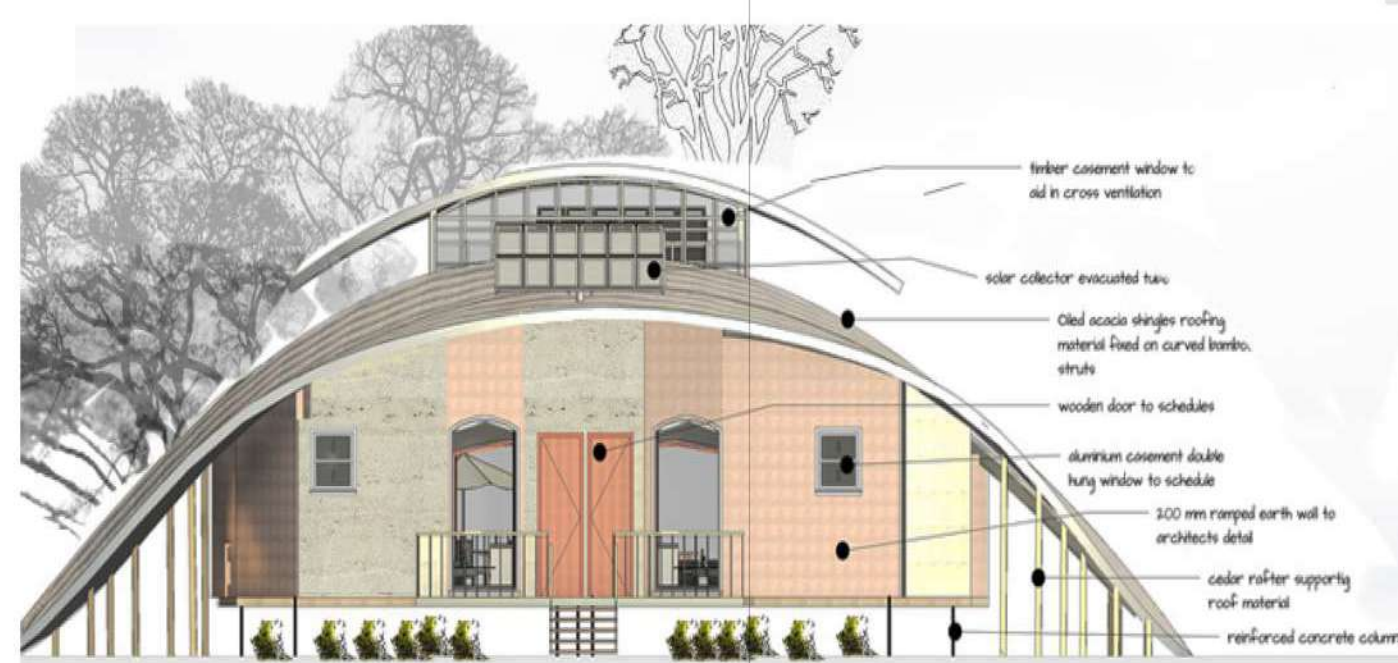

FRONT ELEVATION



BACK ELEVATION

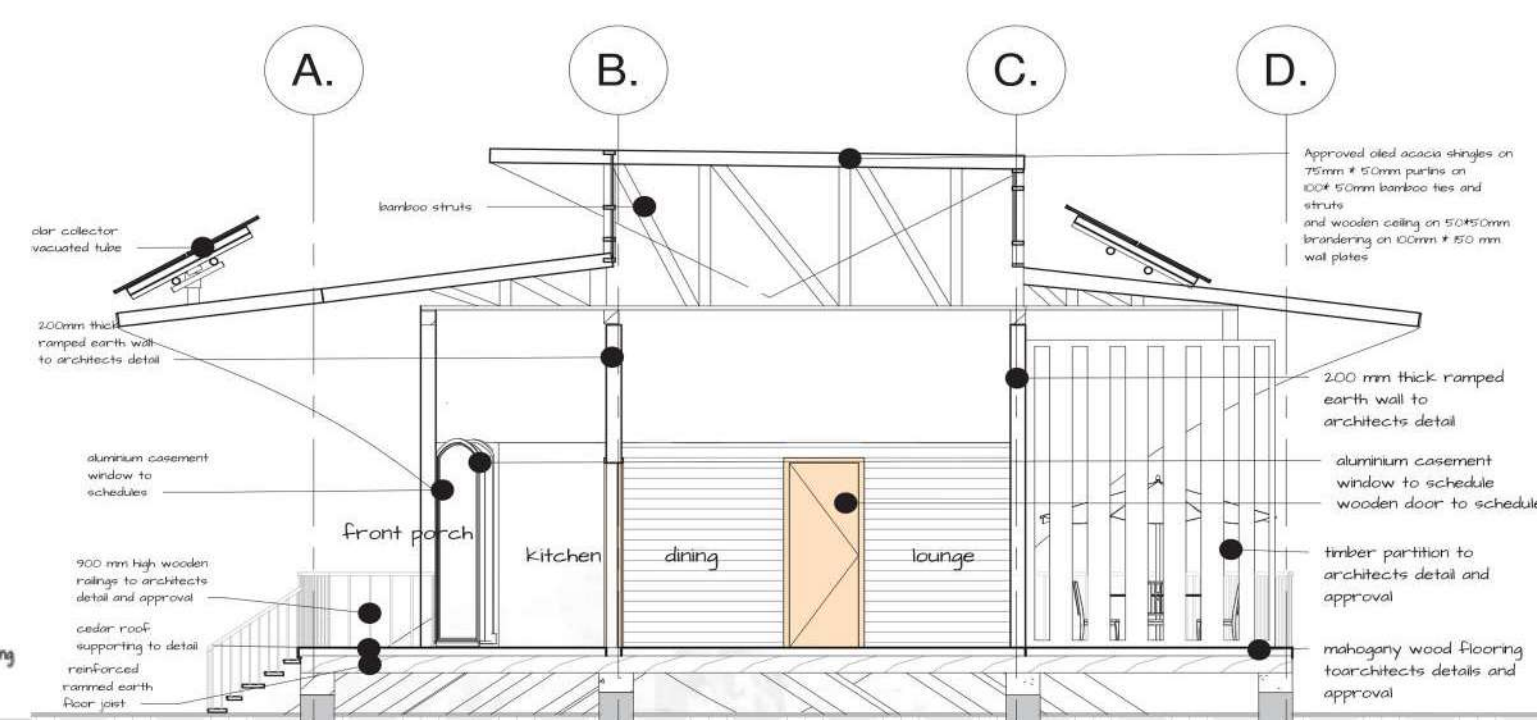

SECTION-01

06: LANDSCAPE DESIGN




outdoor seating area

archives plaza



public pavilion



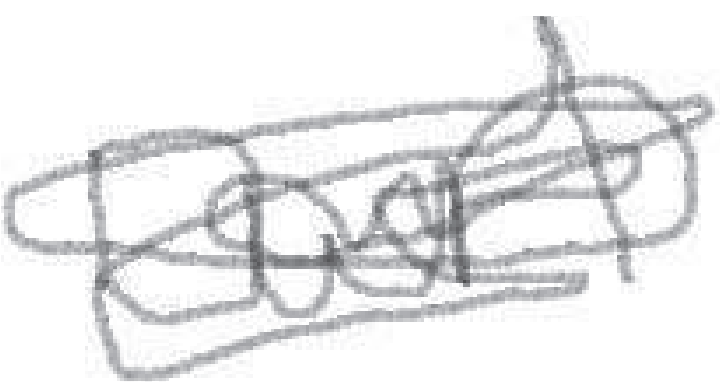

THANK YOU



0743525095



dorisnganga254@gmail.com



[https://www.linkedin.com/in/
doris-ng-ang-a-015b10214](https://www.linkedin.com/in/doris-ng-ang-a-015b10214)



[https://www.instagram.com/
doris.nganga/](https://www.instagram.com/doris.nganga/)